



2131002302

Page: 1 of 2
10/22/2013 12:23 PM
PLAT \$138.00
Whatcom County, WA

Request of: JOAN MARR

PLAT

NUMBER OF SHEETS 2

NAME OF PLAT:

Douglas Place Long Plat Div. 2

DECLARANTS:

Douglas Place LLC

SURVEYOR:

Ronald T. Jepson & Assoc.

SECTION: 30 TOWNSHIP: 39 RANGE: 2E

2131002302

DOUGLAS PLACE LONG PLAT DIV. 2

A PORTION OF THE WEST 1/2 OF THE NORTHWEST 1/4 OF SECTION 30, TOWNSHIP 39 NORTH, RANGE 2 EAST OF W.M.
CITY OF FERNDAL, WHATCOM COUNTY, WASHINGTON STATE

DECLARATION AND DEDICATION

KNOW ALL MEN BY THESE PRESENTS THE UNDERSIGNED, BEING OWNERS IN FEE SIMPLE OF THE LAND HEREIN PLATTED, HEREBY DECLARE AND ACKNOWLEDGE THIS PLAT OF "DOUGLAS PLACE LONG PLAT DIV. 2" AND DEDICATE TO THE USE OF THE PUBLIC FOREVER, ALL ROADS, ALLEYS, EASEMENTS, AND PUBLIC SITES SHOWN ON THIS PLAT; ALSO, THE RIGHT TO MAKE ALL NECESSARY SLOPES FOR CUTS AND FILL UPON LOTS, BLOCKS AND TRACTS IN ANY REASONABLE GRADING OF THE ROADS, ALLEYS, EASEMENTS AND PUBLIC SITES, AND HEREBY WAIVER ALL CLAIMS FOR DAMAGES AGAINST ANY GOVERNMENTAL AUTHORITY WHICH MAY BE OCCASIONED TO ADJACENT LAND BY ESTABLISHED CONSTRUCTION, DRAINAGE, AND MAINTENANCE OF SAID ROAD.

Douglas S. Marr, Manager
DOUGLAS PLACE LLC - A WASHINGTON LIMITED LIABILITY COMPANY
DOUGLAS S. MARR - MANAGER

Joan M. Marr, Manager
DOUGLAS PLACE LLC - A WASHINGTON LIMITED LIABILITY COMPANY
JOAN M. MARR - MANAGER

ACKNOWLEDGMENTS:

STATE OF WASHINGTON }
COUNTY OF WHATCOM }

THIS IS TO CERTIFY THAT ON THE 11 DAY OF October, 2013 BEFORE ME, THE UNDERSIGNED, A NOTARY PUBLIC, HAVE PERSONALLY APPEARED DOUGLAS S. MARR OF DOUGLAS PLACE, A WASHINGTON LIMITED LIABILITY COMPANY, TO ME KNOWN TO BE THE REPRESENTATIVES OF SAID COMPANY WHO EXECUTED THE WITHIN AND FOREGOING DEDICATION AND ACKNOWLEDGED THE SAID INSTRUMENT TO BE THE FREE AND VOLUNTARY ACT AND DEED OF SAID COMPANY FOR THE USES AND PURPOSES THEREIN MENTIONED, AND ON OATH STATED THAT THEY WERE THE INDIVIDUALS AUTHORIZED TO EXECUTE THE SAID INSTRUMENT. WITNESS MY HAND AND OFFICIAL SEAL THE DAY AND YEAR FIRST MENTIONED ABOVE.

Jana Oliver NOTARY PUBLIC IN AND FOR THE
STATE OF WASHINGTON,
RESIDING AT Bellingham.

ACKNOWLEDGMENTS:

STATE OF WASHINGTON }
COUNTY OF WHATCOM }

THIS IS TO CERTIFY THAT ON THE 11 DAY OF October, 2013 BEFORE ME, THE UNDERSIGNED, A NOTARY PUBLIC, HAVE PERSONALLY APPEARED JOAN M. MARR OF DOUGLAS PLACE, A WASHINGTON LIMITED LIABILITY COMPANY, TO ME KNOWN TO BE THE REPRESENTATIVES OF SAID COMPANY WHO EXECUTED THE WITHIN AND FOREGOING DEDICATION AND ACKNOWLEDGED THE SAID INSTRUMENT TO BE THE FREE AND VOLUNTARY ACT AND DEED OF SAID CORPORATION FOR THE USES AND PURPOSES THEREIN MENTIONED, AND ON OATH STATED THAT THEY WERE THE INDIVIDUALS AUTHORIZED TO EXECUTE THE SAID INSTRUMENT. WITNESS MY HAND AND OFFICIAL SEAL THE DAY AND YEAR FIRST MENTIONED ABOVE.

Jana Oliver NOTARY PUBLIC IN AND FOR THE
STATE OF WASHINGTON,
RESIDING AT Bellingham.

NOTES:

- ONE HALF OF THE TRAFFIC IMPACT MITIGATION FEES HAVE BEEN PAID. THE REMAINING HALF SHALL BE PAID PURSUANT TO BUILDING PERMIT CONDITIONS OF APPROVAL. THE SOUTHWEST SEWER BYPASS FEE AND WATER AND SEWER CONNECTION FEES MUST BE PAID PURSUANT TO BUILDING PERMIT CONDITIONS OF APPROVAL. SCHOOL IMPACT FEES WILL BE PAID IN ACCORDANCE WITH THE REQUIREMENTS OF THE FERNDAL SCHOOL DISTRICT.
- EASEMENT NOTE: A 5' UTILITY EASEMENT SHALL BE MAINTAINED AROUND THE PERIMETER OF ALL LOTS PER CITY OF FERNDAL STANDARDS AND 10' UTILITY EASEMENT IS ADOPTED OVER THE FRONT OF ALL LOTS STREET FRONTAGE.
- ALL UTILITY, DRAINAGE, AND ACCESS EASEMENTS SHALL BE WRITTEN IN FAVOR OF THE CITY OF FERNDAL IN ADDITION TO THE OTHER PARTIES REFERENCED.
- LOTS #30, #34, #35 AND #36 WITHIN THIS PLAT SHALL INSTALL A BIORETENTION FACILITY (RAINGARDEN, SEE MAINTENANCE COVENANT) TO ENSURE STORMWATER RUNOFF IS TREATED, DETAINED, AND INFILTRATED. MAINTENANCE COVENANT, ACCESS EASEMENT, AND RAINGARDEN/BIORETENTION DETAIL ARE FILED UNDER 2131002304, AUDITOR'S OFFICE, WHATCOM COUNTY, WASHINGTON.
- RONALD T. JEPSON, THE ENGINEER OF RECORD, HAS PERFORMED DETAILED BIORETENTION ANALYSIS ON THE SITE, AND HAS IDENTIFIED MEASURES TO PREVENT SURFACE RUNOFF AND NON-POINT-SOURCE POLLUTION FROM EXITING THE SITE. DOCUMENTATION TO ASSIST IN DESIGN OF INDIVIDUAL BIORETENTION FACILITIES SHALL BE PROVIDED BY THE ENGINEER OF RECORD FOR EACH BUILDING PERMIT REQUESTED ON THE PLAT.
- ~~ONE HALF OF THE TRAFFIC IMPACT MITIGATION FEES HAVE BEEN PAID. THE REMAINING HALF SHALL BE PAID PURSUANT TO BUILDING PERMIT CONDITIONS OF APPROVAL.~~

AUDITOR'S CERTIFICATE

I HEREBY CERTIFY THAT THIS LONG PLAT WAS FILED FOR RECORD IN THE OFFICE OF THE AUDITOR OF WHATCOM COUNTY, WASHINGTON THIS 22nd DAY OF October, 2013 AT 12:13 A.M. AT THE REQUEST OF

Joan M. Marr AND IS RECORDED UNDER AUDITOR'S FILE NUMBER 2131002302
Dekkie Adelstein
AUDITOR OF WHATCOM COUNTY BY

COVENANTS, CONDITIONS, RESERVATIONS AND RESTRICTIONS

THESE COVENANTS SHALL RUN WITH THE LAND AND SHALL BE REFERENCED ON ANY CONVEYANCES OR AGREEMENTS OF USAGE FOR THE LOTS SHOWN. FILED UNDER

2131002303, AUDITOR'S OFFICE, WHATCOM COUNTY, WASHINGTON.

STORMWATER FACILITY ACCESS

ACCESS TO STORMWATER FACILITIES TO REMAIN UNOBSTRUCTED FOR INSPECTION AND MAINTENANCE OF THE SYSTEM. ACCESS ROADS ARE TO BE MAINTAINED FOR VEHICLE ACCESS. NO ALTERATION IS ALLOWED WITHOUT PRIOR CITY OF FERNDAL APPROVAL.

PLAT ADMINISTRATOR'S APPROVAL

EXAMINED AND APPROVED BY THE PLAT ADMINISTRATOR OF FERNDAL THIS 17th DAY OF October, 2013

J. Oliver
PLAT ADMINISTRATOR, FERNDAL, WASHINGTON

PUBLIC WORKS DIRECTOR'S APPROVAL

EXAMINED AND APPROVED BY THE CITY OF FERNDAL DEPARTMENT OF PUBLIC WORKS THIS 17th DAY OF October, 2013

J. Oliver P.E.
DIRECTOR OF PUBLIC WORKS, FERNDAL, WASHINGTON

CITY CLERK'S APPROVAL

EXAMINED AND APPROVED BY THE FERNDAL CITY CLERK, THIS 11th DAY OF October, 2013

J. Oliver
CITY CLERK, CITY OF FERNDAL, WASHINGTON


MAINTENANCE AGREEMENT

ALL COSTS TO MAINTAIN, REPAIR, IMPROVE ANY STORMWATER FACILITY, DESIGNATED WETLAND, OPEN SPACE TRACT, OR OTHER COMMON FACILITIES OR OPEN SPACE ELEMENTS LOCATED OUTSIDE PUBLIC RIGHT OF WAY SHALL BE BORN BY THE HOMEOWNER'S ASSOCIATION ACCORDING TO THE COVENANTS, CONDITIONS, RESERVATIONS, AND RESTRICTIONS (CC&R'S) OF THE PLAT OF DOUGLAS PLACE LONG PLAT DIV. 2, AS RECORDED UNDER AF # 2131002304, AUDITOR'S OFFICE, WHATCOM COUNTY, WASHINGTON.

COUNTY TREASURER'S CERTIFICATE

I, STEVE OLIVER, TREASURER OF WHATCOM COUNTY, DO HEREBY CERTIFY THAT ALL TAXES REQUIRED BY LAW TO BE PAID UPON THAT PORTION OF REAL ESTATE EMBRACED WITHIN THIS PLAT OF "DOUGLAS PLACE LONG PLAT DIV. 2" AND ALL DELINQUENT ASSESSMENTS HAVE BEEN FULLY PAID AS SHOWN IN THE RECORDS OF MY OFFICE THIS 22nd DAY OF October, 2013

Steve Oliver
STEVE OLIVER TREASURER, WHATCOM COUNTY, WASHINGTON

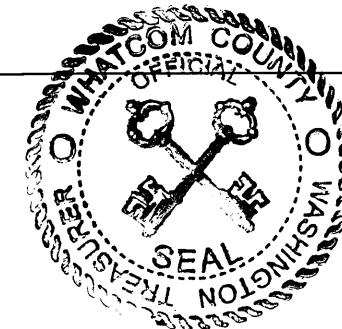


LAND SURVEYOR CERTIFICATION

I HEREBY CERTIFY THAT "DOUGLAS PLACE LONG PLAT DIV. 2" LONG PLAT WAS PREPARED UNDER MY DIRECTION, AND IS BASED UPON AN ACTUAL FIELD SURVEY AT THE REQUEST OF DOUGLAS MARR ON SEPTEMBER, 2013; THAT THE TECHNICAL DATA IS CORRECTLY SHOWN THEREON, AND THAT ALL REQUIRED MONUMENTS AND/OR PARCEL CORNER MARKERS ARE SET.

Ronald T. Jepson
RONALD T. JEPSON L.S. NO. 9361

10/1/13

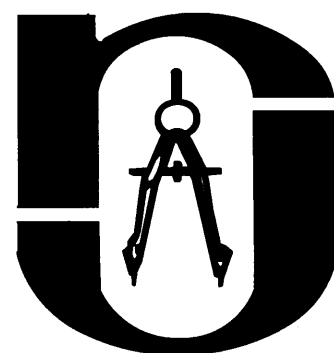

RONALD T. JEPSON & ASSOC.

REGISTERED PROFESSIONAL ENGINEERS AND LAND SURVEYORS | 222 GRAND AVE., SUITE C, BELLINGHAM, WA 98225
PHONE: (360) 733-5760 | FAX: (360) 647-8939 | EMAIL: RJEPSON@JEPSONENGINEERING.COM



Job Number: 12082

Issue Date: 10/8/2013


Page:

1 OF 2

2131002302

DOUGLAS PLACE LONG PLAT DIV. 2

A PORTION OF THE WEST 1/2 OF THE NORTHWEST 1/4 OF SECTION 30, TOWNSHIP 39 NORTH, RANGE 2 EAST OF W.M.
CITY OF FERNDALE, WHATCOM COUNTY, WASHINGTON STATE

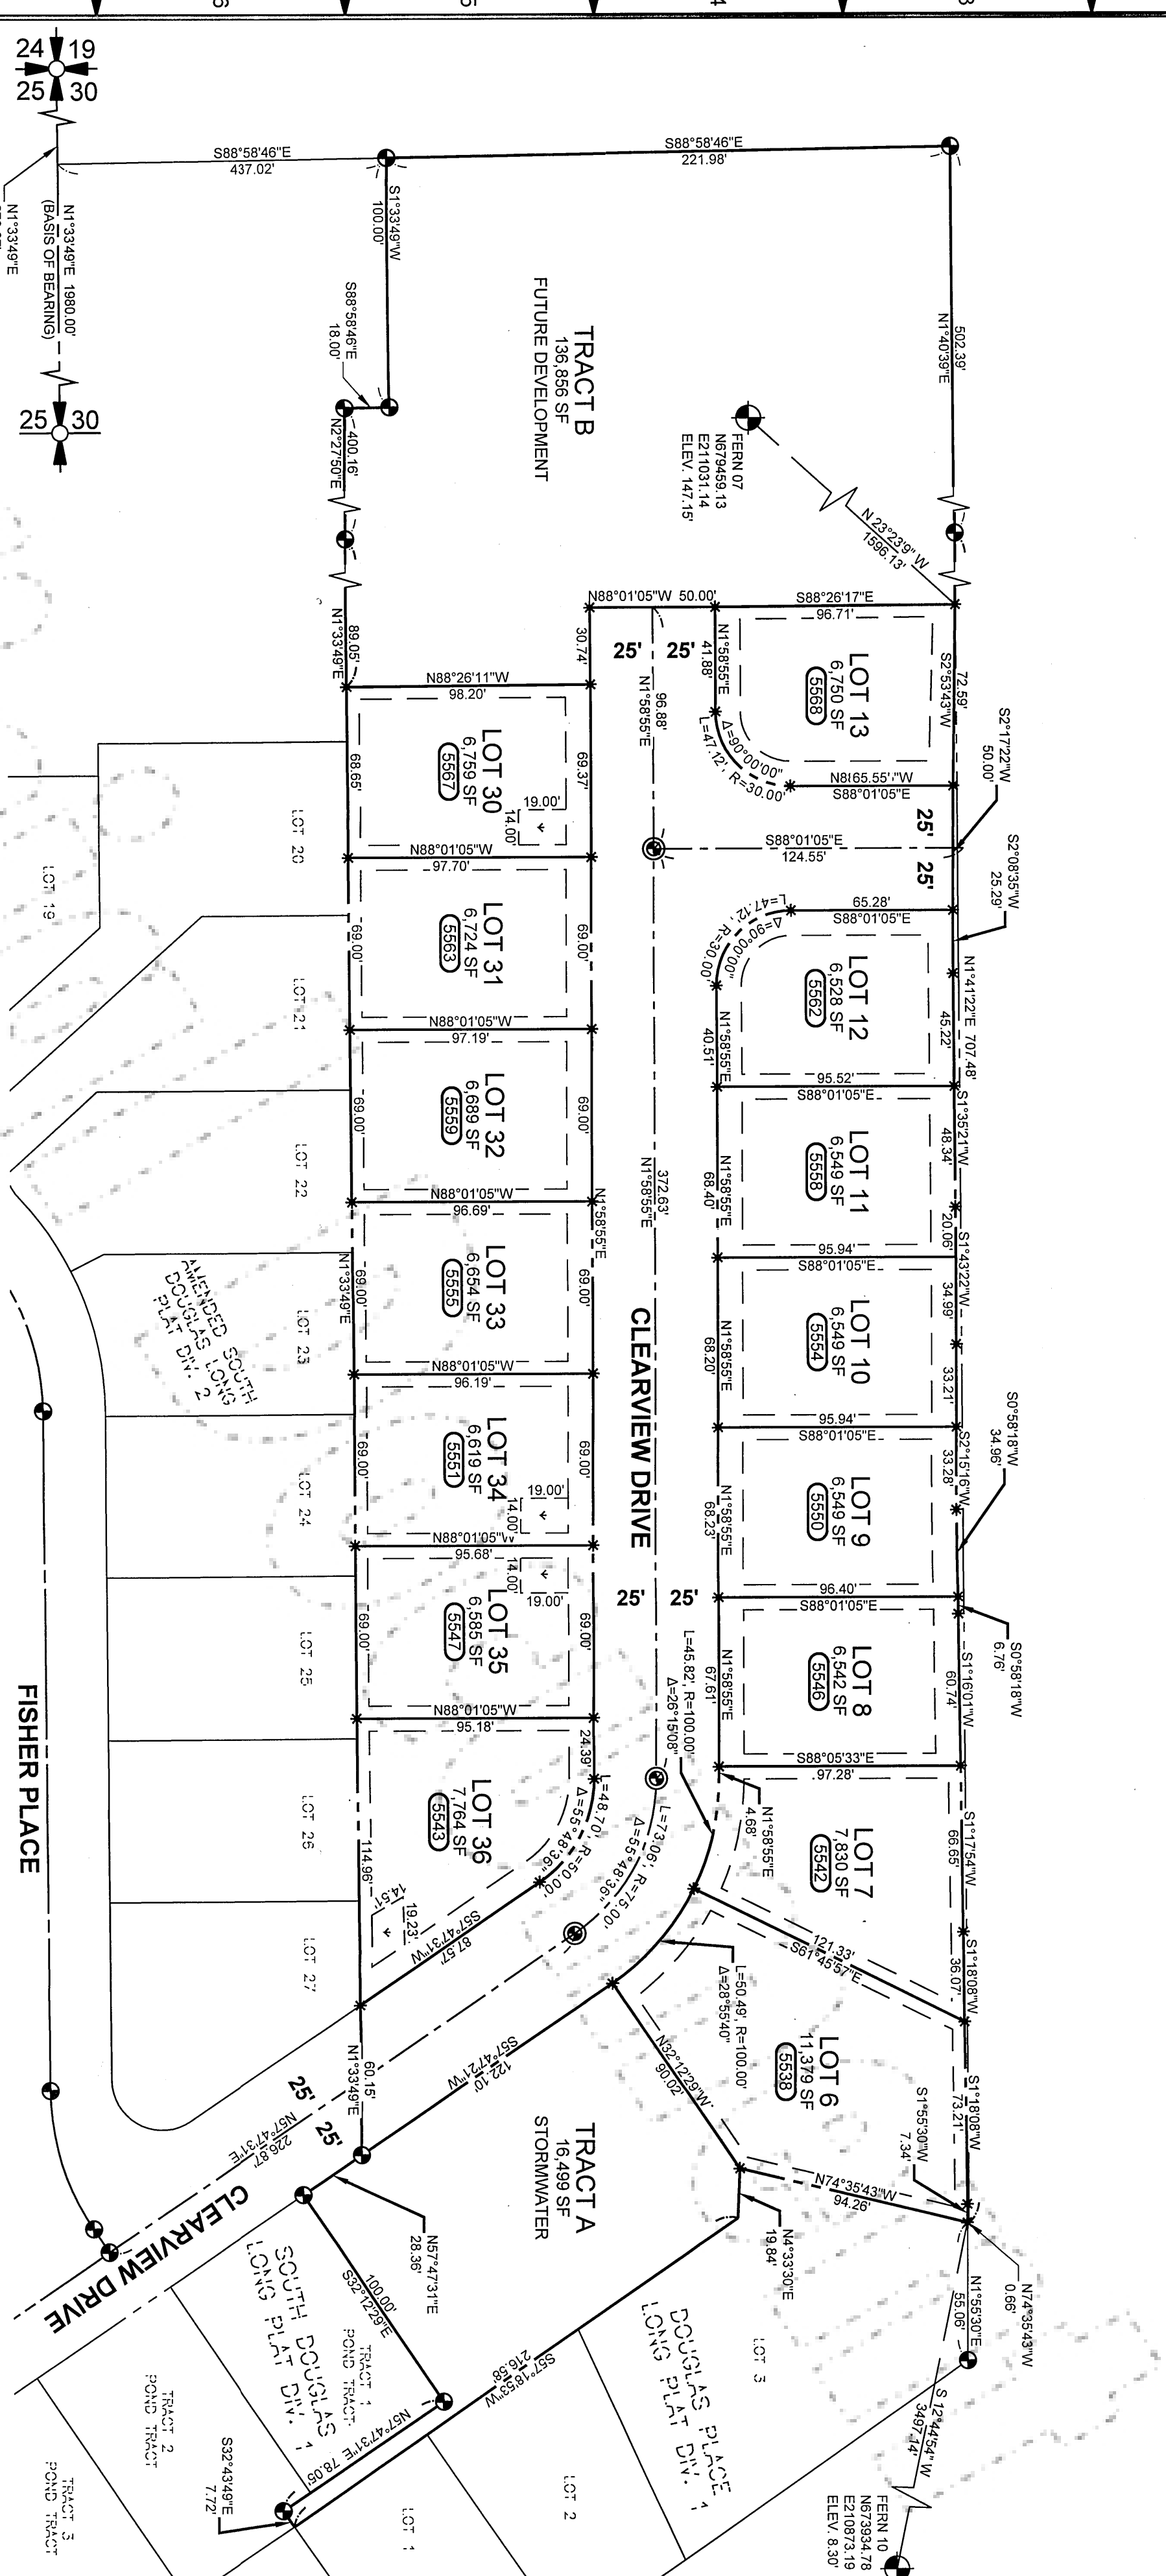

BASIS OF BEARING

THAT RECORD OF SURVEY FILED UNDER WHATCOM COUNTY AF #931119056 BEARING BEING N 07°45'55" W, WEST LINE OF SECTION 30, MONUMENTS AS DEPICTED ON THIS PAGE, ROTATED BEARING OF WEST LINE OF SECTION 30 TO N 08°33'49" E.

DATUM

HORIZONTAL: NAD 83/81
VERTICAL: NGVD 29

SURVEY EQUIPMENT AND PROCEDURE

THIS SURVEY WAS COMPLETED AND ACCOMPISHED BY FIELD TRAVERSE USING A NIKON DTM-521 TOTAL STATION IN AUGUST 2013.

LEGAL DESCRIPTION

TRACT 1 OF DOUGLAS PLACE LONG PLAT DIV. 1
RECORDED UNDER AF #2110101245.

NOTES

- SUBJECT TO COVENANTS AND RESTRICTIONS FILED UNDER AF # 2131002304
- SUBJECT TO RECIPROCAL STORMWATER FACILITIES EASEMENT FILED UNDER AF #2090102035.
- RIGHT OF WAY & UTILITY EASEMENT FILED UNDER AF #2090604157

LEGEND

- FOUND SECTION CORNER
- FOUND 1/4 SEC CORNER
- FOUND BASS DISK IN CONC. MON.
- SET REBAR & CAP #9361
- SET BRASS DISK IN CONC. MON.
- RAINGARDEN EASEMENT

RONALD T. JEPSON & ASSOC.
REGISTERED PROFESSIONAL ENGINEERS AND LAND SURVEYORS | 222 GRAND AVE., SUITE C, BELLINGHAM, WA 98225
PHONE: (360) 733-5760 | FAX: (360) 647-8939 | EMAIL: RJEPSON@JEPSONENGINEERING.COM

12082

0 50 100
SCALE: 1" = 50'

Job Number:	12082
Issue Date:	10/6/2013

Page: 2 OF 2