



00107215201712021330030032

PLAT: Douglas Place Long Plat Division 3

Number of Pages: 3

Grantor (Declarants):

Douglas Place LLC

Grantee: Public

Quarter: NW

Quarter: NW

Gov't Lot:

Section: 30

Township: 39N

Range: 02E

2017-1202133

DOUGLAS PLACE LONG PLAT DIVISION 3

PLAT NO. _____

BEING A PORTION OF THE NORTHWEST 1/4 OF THE NORTHWEST 1/4 OF SECTION 30, TOWNSHIP 39 NORTH, RANGE 2 EAST OF W.M.
CITY OF FERNDAL, WHATCOM COUNTY, WASHINGTON

LEGAL DESCRIPTION

(PER CHICAGO TITLE INSURANCE COMPANY GUARANTEE/CERTIFICATE NO. 245397824, DATED NOVEMBER 8, 2017)

TRACT B, DOUGLAS PLACE LONG PLAT DIV. 2, ACCORDING TO THE PLAT THEREOF, RECORDED OCTOBER 22, 2013, UNDER AUDITOR'S FILE NO. 213-1002302, RECORDS OF WHATCOM COUNTY, WASHINGTON.

SITUATE IN WHATCOM COUNTY, WASHINGTON.

DECLARATION AND DEDICATION

KNOWN TO ALL PERSONS BY THESE PRESENTS THAT WE THE UNDERSIGNED, BEING OWNERS IN FEE SIMPLE OF THE LAND HEREIN PLATTED, ARE PERSONS AUTHORIZED BY ALL PARTIES HAVING ANY INTEREST IN THE LAND HEREON DESCRIBED TO OBTAIN THIS PLAT, HEREBY DECLARE AND ACKNOWLEDGE THIS "DOUGLAS PLACE LONG PLAT DIVISION 3" AND DEDICATE TO THE USE OF THE PUBLIC FOREVER ALL ROADS AND/OR RIGHTS-OF-WAY OR OTHER AREAS AND OTHER WAYS; DO HEREBY WAIVE ON BEHALF OF THEMSELVES AND THEIR SUCCESSORS IN INTEREST ALL CLAIMS FOR DAMAGES AGAINST THE CITY OF FERNDAL AND ANY OTHER GOVERNMENTAL AUTHORITY WHICH MAY BE OCCASIONED TO THE ADJACENT LAND BY THE ESTABLISHED CONSTRUCTION, DRAINAGE AND MAINTENANCE OF SAID DEDICATED ROADS AND/OR RIGHTS-OF-WAY OR OTHER AREAS AND OTHER WAYS, AND DO HEREBY GRANT AND RESERVE ANY EASEMENTS SHOWN HEREON FOR THE USES INDICATED.

Douglas S. Marr
DOUGLAS PLACE LLC, A WASHINGTON LIMITED LIABILITY COMPANY
DOUGLAS S. MARR, MANAGER

Joan M. Marr
DOUGLAS PLACE LLC, A WASHINGTON LIMITED LIABILITY COMPANY
JOAN M. MARR, MANAGER

ACKNOWLEDGEMENT


STATE OF WASHINGTON } SS
COUNTY OF WHATCOM }

I HEREBY CERTIFY THAT I KNOW OR HAVE SATISFACTORY EVIDENCE THAT DOUGLAS S. MARR IS THE PERSON WHO APPEARED BEFORE ME, AND SAID PERSON ACKNOWLEDGED THAT HE SIGNED THIS INSTRUMENT, ON OATH STATED THAT HE WAS AUTHORIZED TO EXECUTE THE INSTRUMENT AND ACKNOWLEDGED IT AS THE MANAGER OF DOUGLAS PLACE LLC, A WASHINGTON LIMITED LIABILITY COMPANY, TO BE THE FREE AND VOLUNTARY ACT OF SUCH PARTY FOR THE USES AND PURPOSES MENTIONED IN THE INSTRUMENT.

GIVEN UNDER MY HAND AND OFFICIAL SEAL THIS 14th DAY OF December, 2017

Terry A. Unger
NOTARY PUBLIC IN AND FOR THE STATE OF WASHINGTON

RESIDING AT Bellingham WA

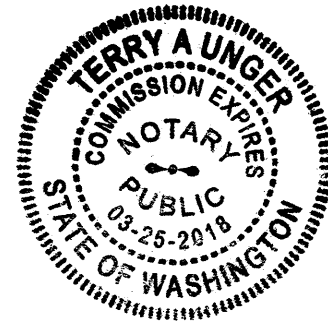

ACKNOWLEDGEMENT


STATE OF WASHINGTON } SS
COUNTY OF WHATCOM }

I HEREBY CERTIFY THAT I KNOW OR HAVE SATISFACTORY EVIDENCE THAT JOAN M. MARR IS THE PERSON WHO APPEARED BEFORE ME, AND SAID PERSON ACKNOWLEDGED THAT SHE SIGNED THIS INSTRUMENT, ON OATH STATED THAT SHE WAS AUTHORIZED TO EXECUTE THE INSTRUMENT AND ACKNOWLEDGED IT AS THE MANAGER OF DOUGLAS PLACE LLC, A WASHINGTON LIMITED LIABILITY COMPANY, TO BE THE FREE AND VOLUNTARY ACT OF SUCH PARTY FOR THE USES AND PURPOSES MENTIONED IN THE INSTRUMENT.

GIVEN UNDER MY HAND AND OFFICIAL SEAL THIS 14th DAY OF December, 2017

Terry A. Unger
NOTARY PUBLIC IN AND FOR THE STATE OF WASHINGTON

RESIDING AT Bellingham WA

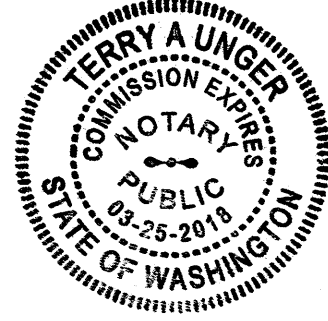

COVENANTS, CONDITIONS AND RESTRICTIONS

THE DECLARATION OF COVENANTS, CONDITIONS, RESTRICTIONS AND RESERVATIONS FOR "DOUGLAS PLACE DIVISION 3 LONG PLAT" ARE RECORDED UNDER AUDITOR'S FILE NO. 2017-1202134.

MAINTENANCE AGREEMENT

ALL COSTS TO MAINTAIN, REPAIR, IMPROVE ANY STORMWATER FACILITY, DESIGNATED WETLAND, OPEN SPACE TRACT, OR OTHER COMMON FACILITIES OR OPEN SPACE ELEMENTS LOCATED OUTSIDE PUBLIC RIGHT-OF-WAY SHALL BE BORN BY THE HOMEOWNER'S ASSOCIATION ACCORDING TO THE COVENANTS, CONDITIONS, RESERVATIONS, AND RESTRICTIONS (CC&R'S) OF DOUGLAS PLACE LONG PLAT DIVISION 3, AS RECORDED UNDER AUDITOR'S FILE NO. 2090102035, RECORDS OF WHATCOM COUNTY, WASHINGTON.


STORMWATER NOTE

ALL LOTS IN THIS LONG PLAT ARE ALLOWED A TOTAL OF 2500 SQ. FT. OF IMPERVIOUS SURFACE WHICH INCLUDES ROOF AREA AND DRIVEWAYS.


STORMWATER MANAGEMENT AND SITE DESIGN MUST BE DONE IN ACCORDANCE WITH THE STORMWATER SITE PLAN FOR DOUGLAS PLACE LONG PLAT AND SOUTH DOUGLAS LONG PLAT PREPARED BY RONALD T. JEPSON AND ASSOCIATES DATED MAY 2017.

ALL DISRUPTED SOILS WITHIN THIS LONG PLAT SHALL BE AMENDED PER BMP T5.13 - POST CONSTRUCTION SOIL QUALITY AND DEPTH, PER THE AFOREMENTIONED STORMWATER SITE PLAN FOR DOUGLAS PLACE LONG PLAT AND SOUTH DOUGLAS LONG PLAT.

BUILDING APPLICATIONS MUST INCLUDE DETAIL FOR BMP T5.13 POST CONSTRUCTION SOIL QUALITY AND DEPTH BEFORE SUBMITTAL. THE ENGINEER OF RECORD WILL CERTIFY INSTALLATION, INCLUDING SOILS ANALYSIS AND CERTIFICATION OF COMPOST AMENDMENT, PRIOR TO FINAL OCCUPANCY.

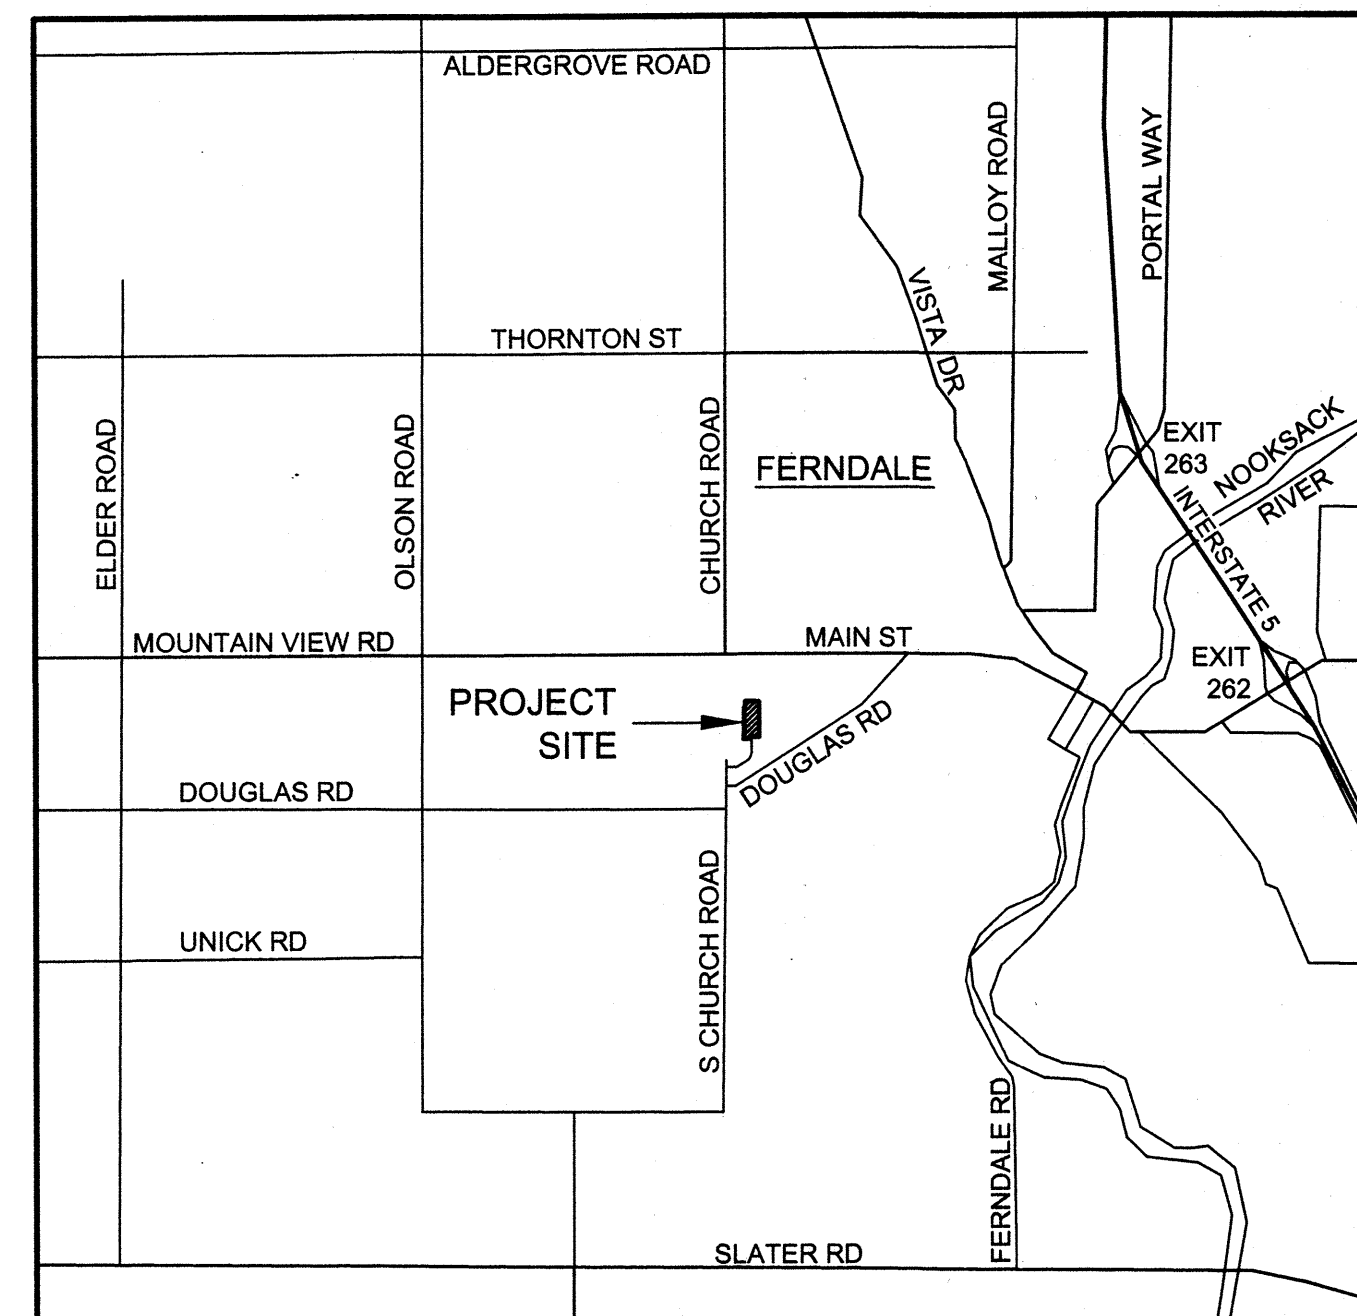

VICINITY MAP

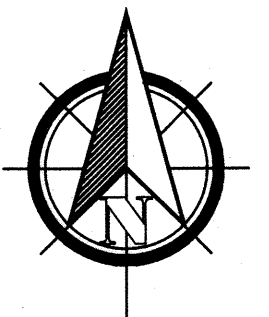

NOT TO SCALE

NOTES:

1. ALL OR ANY LOTS REQUIRING MORE THAN THE 1-FOOT MINIMUM FILL AMOUNT WILL REQUIRE STRUCTURAL FILL DOCUMENTATION BY A LICENSED GEOTECHNICAL ENGINEER.
2. ALL LOTS HAVE A 10' UTILITY EASEMENT ADJACENT TO PUBLIC RIGHT-OF-WAYS AND A 5' UTILITY EASEMENT ALONG ALL OTHER SIDES UNLESS A WIDER EASEMENT IS SHOWN ON THE PLAN.
3. FUTURE LOT OWNERS SHALL ADDRESS APPENDIX J INTERNATIONAL BUILDING CODE REQUIREMENTS.
4. HALF OF THE TRAFFIC, PARK AND SCHOOL IMPACT FEES HAVE BEEN PAID, THE REMAINING HALF SHALL BE PAID PURSUANT TO BUILDING PERMIT CONDITIONS OF APPROVAL. SCHOOL IMPACT FEES SHALL BE PAID IN ACCORDANCE WITH THE REQUIREMENTS OF THE FERNDAL SCHOOL DISTRICT. STORM SEWER MITIGATION FEES PER SQUARE FOOT OF GROSS PROPERTY AREA HAVE BEEN PAID. WATER AND SEWER CONNECTION FEES SHALL BE PAID PURSUANT TO BUILDING PERMIT CONDITIONS OF APPROVAL.
5. SUBJECT TO RECIPROCAL STORMWATER FACILITIES EASEMENT FILED UNDER AUDITOR'S FILE NO. 2090102035.
6. SUBJECT TO RIGHT-OF-WAY & UTILITY EASEMENT FILED UNDER AUDITOR'S NO. 2090604157
7. SUBJECT TO PUGET SOUND ENERGY EASEMENT FILED UNDER AUDITOR'S FILE NO. 2150602829.

PUBLIC WORKS DIRECTOR'S APPROVAL

EXAMINED AND APPROVED BY THE CITY OF FERNDAL DEPARTMENT OF PUBLIC WORKS AS TO THE SURVEY DATA, LAYOUT OF ROADS AND OTHER RIGHT-OF-WAYS THIS 15th DAY OF December, 2017.

[Signature]
PUBLIC WORKS DIRECTOR, CITY OF FERNDAL, WASHINGTON

PLAT ADMINISTRATOR APPROVAL

EXAMINED AND APPROVED BY THE CITY OF FERNDAL PLAT ADMINISTRATOR THIS 15th DAY OF December, 2017.

[Signature]
PLAT ADMINISTRATOR, CITY OF FERNDAL, WASHINGTON

CITY CLERK'S APPROVAL

THIS PLAT APPROVED AND ROADS ACCEPTED BY ORDER OF THE CITY CLERK OF FERNDAL, WASHINGTON THIS 18th DAY OF December, 2017.

[Signature]
CITY CLERK, CITY OF FERNDAL, WASHINGTON



WHATCOM COUNTY TREASURER'S CERTIFICATE

I, STEVE OLIVER, TREASURER OF WHATCOM COUNTY, WASHINGTON, DO HEREBY CERTIFY THAT ALL TAXES REQUIRED BY LAW TO BE PAID UPON THE REAL ESTATE EMBRACED WITHIN THIS PLAT OF "DOUGLAS PLACE DIVISION 3" AND ALL DELINQUENT ASSESSMENTS HAVE BEEN FULLY PAID. AS SHOWN IN THE RECORDS OF MY OFFICE, THIS 19th DAY OF December, 2017.

[Signature]
TREASURER
WHATCOM COUNTY WASHINGTON

AUDITOR'S CERTIFICATE

FILED FOR RECORD THIS 19th DAY OF December, 2017

AT 2:15 P.M. UNDER AFF# 2017-1202133


AT THE REQUEST OF Ronald T. Jepson

Debbie Adalstein by Krystal Ross
COUNTY AUDITOR

LAND SURVEYOR CERTIFICATION

THIS MAP CORRECTLY REPRESENTS A SURVEY MADE BY ME OR UNDER MY DIRECTION IN CONFORMANCE WITH THE REQUIREMENTS OF THE STATE LAW AT THE REQUEST OF DOUGLAS S. MARR IN AUGUST, 2017.

[Signature]
RONALD T. JEPSON
L.S. NO. 9361

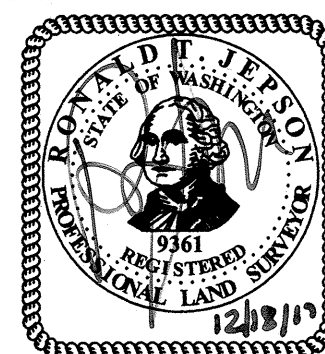

PREPARED FOR: DOUG MARR
PTN. NW 1/4 NW 1/4 SEC. 30, TWP. 39 N., RGE. 2 E. W.M.



RONALD T. JEPSON & ASSOC.
REGISTERED PROFESSIONAL ENGINEERS AND LAND SURVEYORS
222 GRAND AVE., SUITE C, BELLINGHAM, WA 98225
PHONE: (360) 733-5760
FAX: (360) 647-8939
EMAIL: RJEPSON@JEPSONENGINEERING.COM

DOUGLAS PLACE LONG PLAT DIV. 3

PTN. NW 1/4 NW 1/4 SEC. 30, TWP. 39 N., RGE. 2 E. W.M.
CITY OF FERNDAL, WHATCOM COUNTY, WA.

JOB NO: 12082.04	ISSUE DATE: 12/12/2017	SHEET NO.: 1 of 3
DRAWN BY: DRM	CHECKED BY: RTJ	

2017-1202133

DOUGLAS PLACE LONG PLAT DIVISION 3

BEING A PORTION OF THE NORTHWEST 1/4 OF THE NORTHWEST 1/4
OF SECTION 30, TOWNSHIP 39 NORTH, RANGE 2 EAST OF W.M.
CITY OF FERNDAL, WHATCOM COUNTY, WASHINGTON

PLAT NO. _____

NORTHWEST CORNER
SECTION 30-39N-2E
POSITION PER PER
DOUGLAS PLACE
LONG PLAT DIV. 2
(AF NO. 2131002302)

MOUNTAIN VIEW RD.

CITY OF FERNDAL SURVEY
MONUMENT NETWORK
STATION FERN07
N 679459.13
E 1211031.14

PHEIFER SHORT PLAT
LOT 3 LOT 4

MOUNTAIN VIEW
MEADOWS PLAT
OPEN SPACE
TRACT "A"

S88° 58' 46"E - 659.00' [600.00' PER ROS (AF NO. 931119056)]

CITY LIMITS PER
ORDINANCE NO. 1184
(AF NO. 1980202668)

SOUTH

TRACT A1

DOUGLAS

LOT 11
LOT 10
LOT 9
LOT 8
LOT 7
LOT 6
LOT 5
LOT 4
LOT 3
LOT 2
LOT 1

S1° 33' 49"W - 2653.07' [BASIS OF BEARINGS]
875.04'

S. CHURCH RD.

LOT 10
LOT 9
LOT 8
LOT 7
LOT 6
LOT 5
LOT 4
LOT 3
LOT 2
LOT 1

N88° 58' 46"W
15.98'

1226.54'

320.52'


N3° 42' 28"E - 265.07'

S88° 26' 11"E
4.50'

WEST 1/4 CORNER
SECTION 30-39N-2E
POSITION PER PER
DOUGLAS PLACE
LONG PLAT DIV. 2
(AF NO. 2131002302)

CITY OF FERNDAL SURVEY
MONUMENT NETWORK
STATION FERN10
N 673934.78
E 1210873.19

LINE AND CURVE TABLE			
NUMBER	LENGTH	DIRECTION OR DELTA	RADIUS
C3	115.99'	33°3'43"	200.00'
C4	58.94'	33°46'18"	100.00'
C5	81.16'	46°30'10"	100.00'
C6	73.06'	55°48'36"	75.00'
C1	55.81'	103°57"	3000.00'
C2	55.97'	104°08"	3000.00'
C7	119.07'	90°57'41"	75.00'
L1	121.28'	S88°58'46"E	
L2	11.21'	N32°12'29"W	
L3	53.53'	N44°56'21"W	
L4	120.41'	S88°01'05"E	
L5	25.00'	S2°17'22"W	
L6	72.59'	S2°53'43"W	
L7	50.00'	N88°01'05"W	
L8	44.44'	N88°58'46"W	
L9	18.00'	N88°58'46"W	
L10	100.00'	N1°33'49"E	
L11	58.67'	N1°41'22"E	
L12	96.71'	S88°26'17"E	
L13	30.74'	N1°58'55"E	
L14	89.05'	S1°33'49"W	
L14	98.20'	S88°26'11"E	
L15	21.85'	S1°33'49"W	
L16	100.00'	N88°26'11"W	
L17	12.92'	S1°33'49"W	
L18	150.00'	S88°26'11"E	
L19	162.72'	N88°58'46"W	

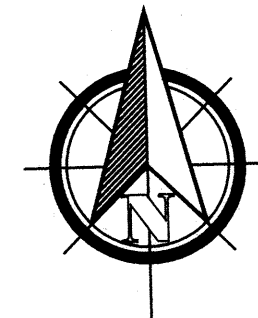

0 100 200
SCALE: 1" = 100'

REFERENCE SURVEYS


NAME	AF NO.	ROTATION USED
PHEIFER SHORT PLAT	1484322	1°33'49"
MOUNTAIN VIEW MEADOWS PLAT	2060504943	0°00'04"
SOUTH DOUGLAS LONG PLAT DIV. 1	2090102033	0°12'06"
AMD. SOUTH DOUGLAS LONG PLAT DIV. 2	2121003585	0°12'06"
SOUTH DOUGLAS LONG PLAT DIV. 3	2150201460	0°12'06"
SOUTH DOUGLAS LOT LINE ADJUSTMENT	2090701534	0°12'06"
DOUGLAS PLACE LONG PLAT DIV. 1	2110101245	0°12'06"
DOUGLAS PLACE LONG PLAT DIV. 2	2131002302	0°12'06"
RECORD OF SURVEY	931119056	0°12'06"

SURVEYOR'S NOTES:


- STANDARD FIELD TRAVERSE PROCEDURES PERFORMED WITH A LEICA 1203 ROBOTIC TOTAL STATION WAS USED TO ACCOMPLISH THIS SURVEY, WHOSE ACCURACY MEETS OR EXCEEDS THOSE PRECISION STANDARDS STATED IN WAC 332-130-090.
- THE FIELD WORK PERFORMED FOR THIS SURVEY WAS COMPLETED OCTOBER 18, 2017. ALL MONUMENTS SHOWN HEREON WERE VISITED DURING THE COURSE OF THIS SURVEY UNLESS OTHERWISE NOTED.
- HORIZONTAL DATUM: CITY OF FERNDAL SURVEY CONTROL NETWORK (NAD 83/91).
- BASIS OF BEARINGS: DOUGLAS PLACE LONG PLAT DIVISION NO. 2, ACCORDING TO THE PLAT THEREOF, RECORDED OCTOBER 22, 2013, UNDER AUDITOR'S FILE NO. 2131002302, RECORDS OF WHATCOM COUNTY, WASHINGTON.
LINE HELD: NORTH 1°58'55" EAST - 372.36' ALONG THE CENTERLINE OF CLEARVIEW DRIVE BETWEEN FOUND BRASS DISK SURFACE MONUMENTS (AS SHOWN)
- THIS SURVEY DEPICTS OCCUPATIONAL INDICATORS IN ACCORDANCE WITH WAC 332.130. THESE OCCUPATIONAL INDICATORS MAY INDICATE A POTENTIAL CLAIM OF UNWRITTEN OWNERSHIP. THE LEGAL RESOLUTION OF SUCH CLAIMS HAS NOT BEEN RESOLVED BY THIS SURVEY.

LEGEND

- ⊕ FOUND 2" BRASS-DISK SURFACE MONUMENT
- ⊕ FOUND 3" BRASS DISK PLAT BOUNDARY MONUMENT (P.L.S. NO. 9361)
- ⊕ FOUND 3" ALUMINUM DISK PLAT BOUNDARY MONUMENT (P.L.S. NO. 40525)
- FOUND 1/2" REBAR WITH YELLOW CAP (P.L.S. NO. 9361)
- SET 2" BRASS DISK SURFACE MONUMENT (P.L.S. NO. 9361)
- ⊕ SET 3" BRASS DISK PLAT BOUNDARY MONUMENT (P.L.S. NO. 9361)
- ⊕ BRASS DISK SURFACE MONUMENT PER AMD. SOUTH DOUGLAS LONG PLAT DIV. 2 (AF NO. 2121003585)
- ⊕ BRASS DISK SURFACE MONUMENT PER SOUTH DOUGLAS LONG PLAT DIV. 1 (AF NO. 2090102033)
- ⊕ CALCULATED 1/16 CORNER POSITION

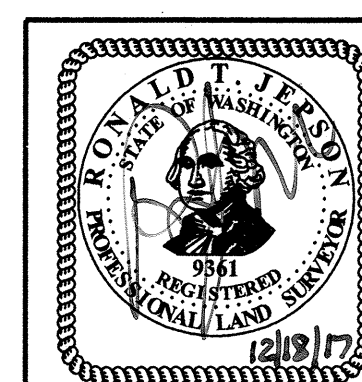

PREPARED FOR: DOUG MARR
PTN. NW 1/4 NW 1/4 SEC. 30, TWP. 39 N., RGE. 2 E. W.M.

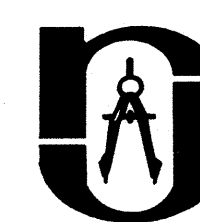


RONALD T. JEPSON & ASSOC.
REGISTERED PROFESSIONAL ENGINEERS AND LAND SURVEYORS
222 GRAND AVE., SUITE C, BELLINGHAM, WA 98225
PHONE: (360) 733-5760
FAX: (360) 647-8939
EMAIL: RJEPSON@JEPSONENGINEERING.COM

DOUGLAS PLACE LONG PLAT DIV. 3
PTN. NW 1/4 NW 1/4 SEC. 30, TWP. 39 N., RGE. 2 E. W.M.
CITY OF FERNDAL, WHATCOM COUNTY, WA.

JOB NO: 12082.04	ISSUE DATE: 12/12/2017	SHEET NO.: 2 of 3
DRAWN BY: DRM	CHECKED BY: RTJ	

2017-1202133

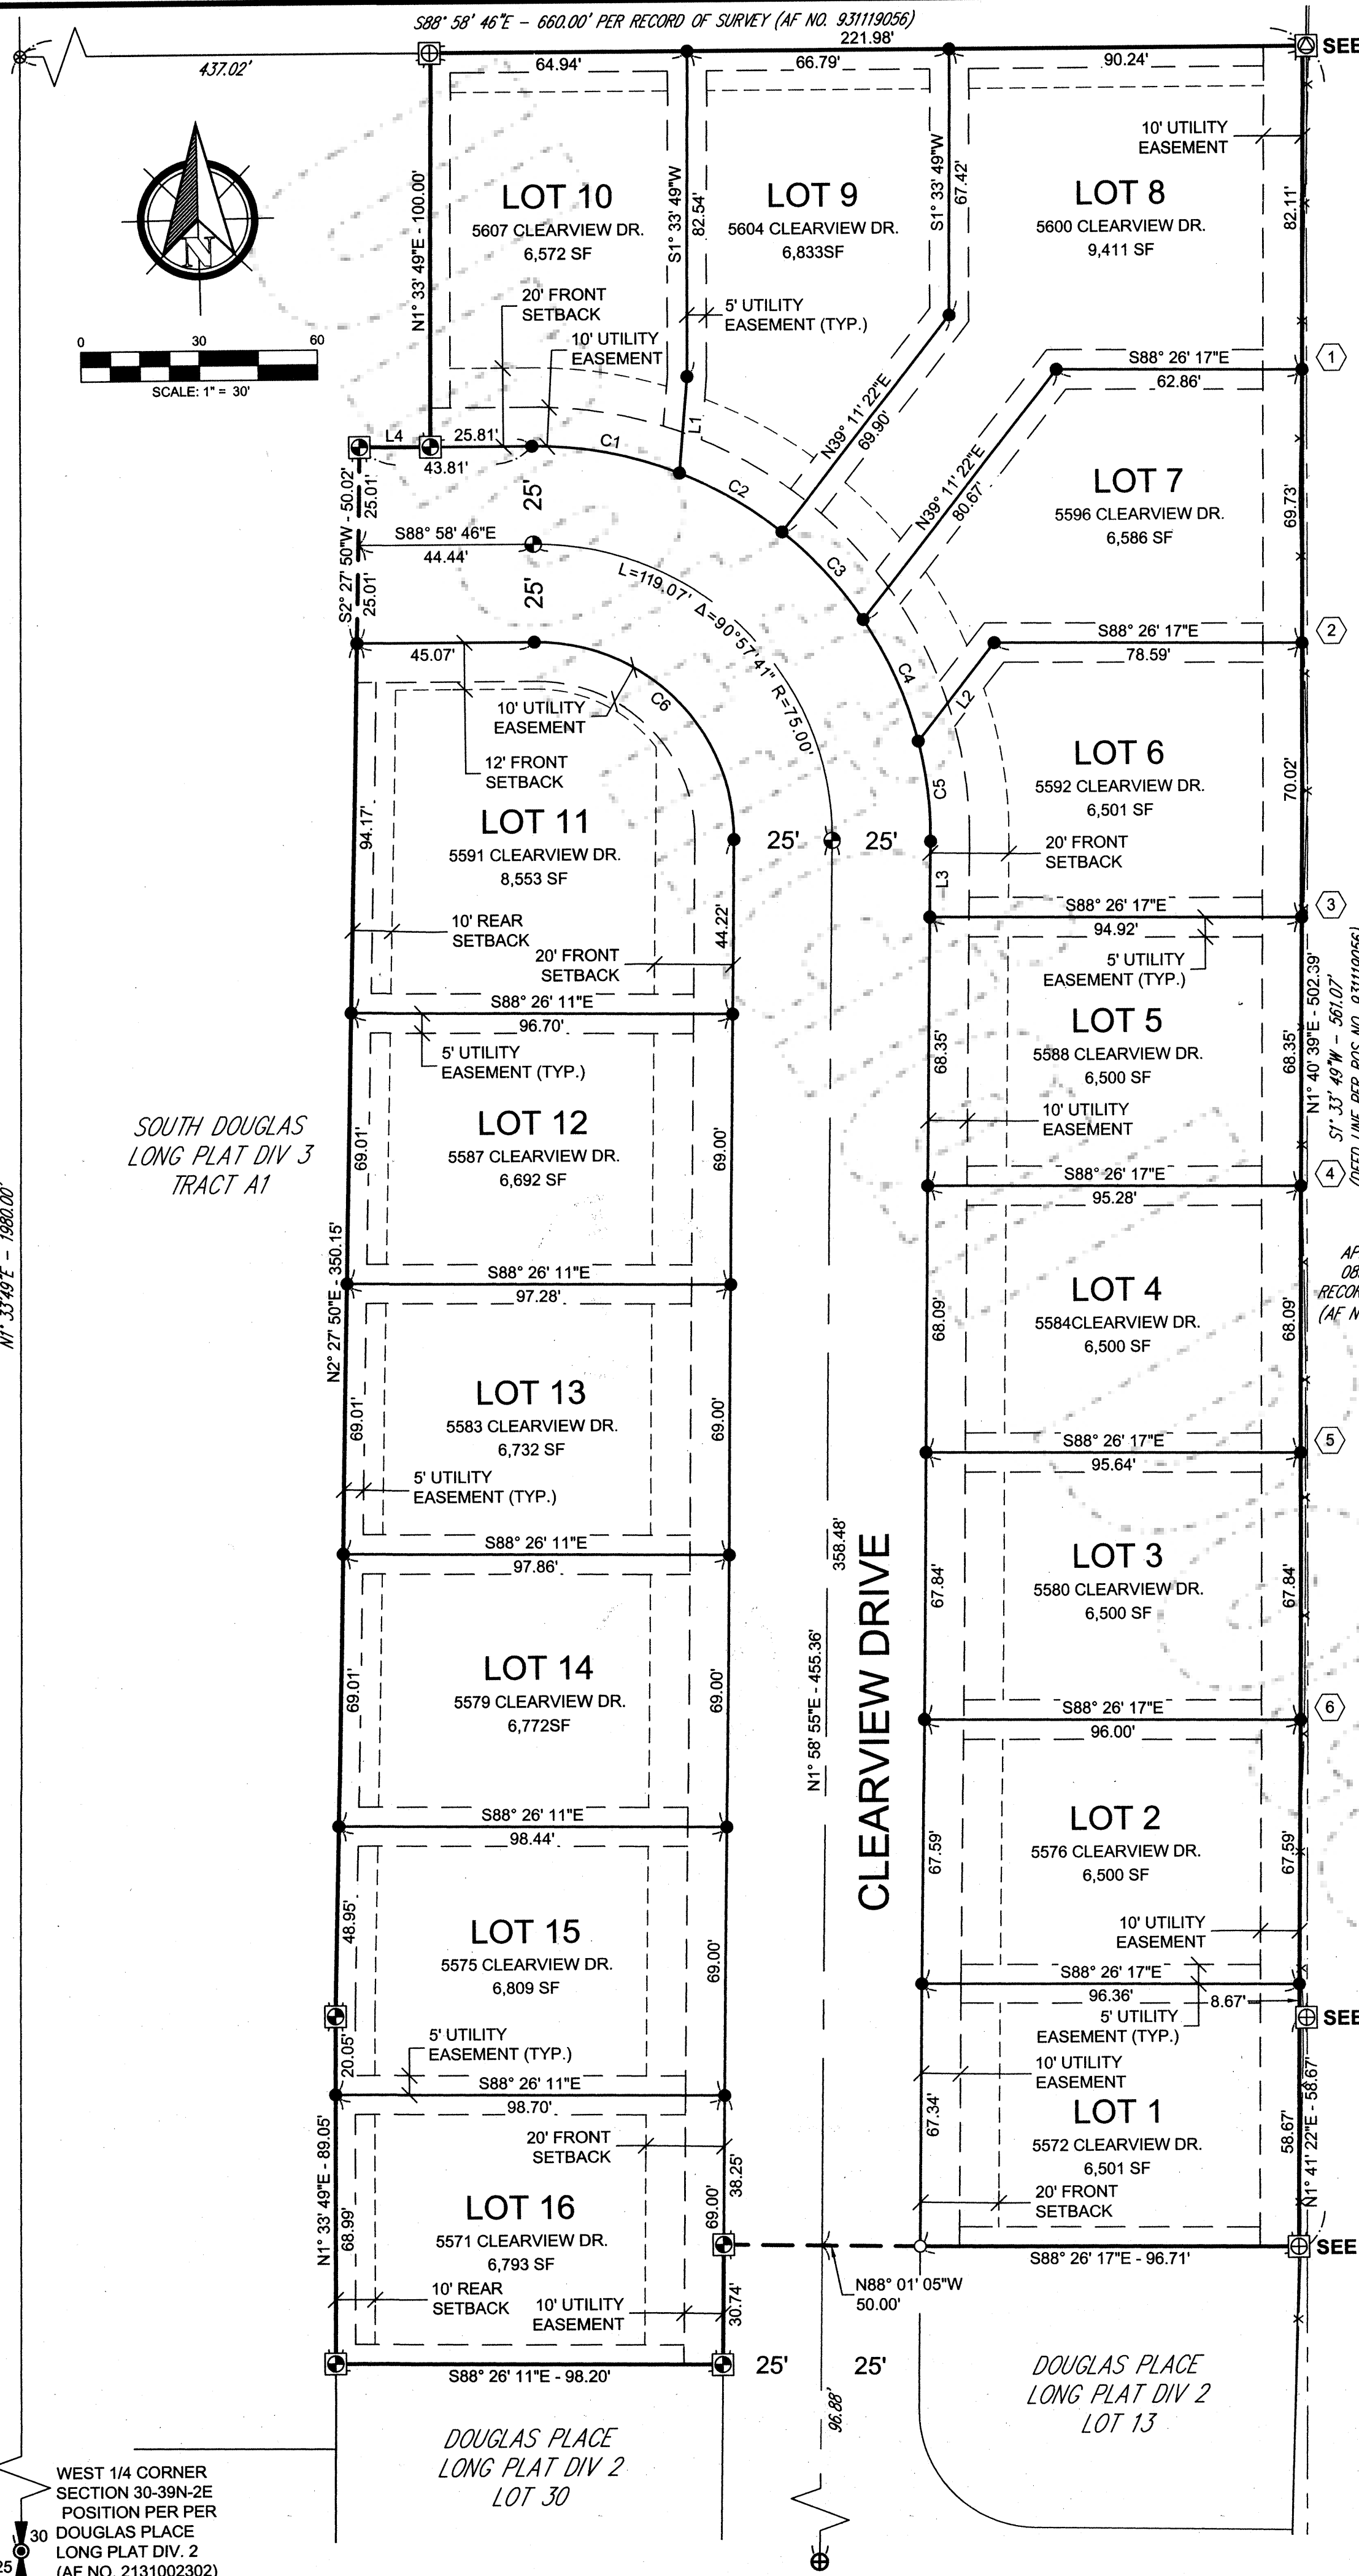

PLAT NO. _____

DOUGLAS PLACE LONG PLAT DIV. 3

BEING A PORTION OF THE NORTHWEST 1/4 OF THE NORTHWEST 1/4 OF SECTION 30, TOWNSHIP 39 NORTH, RANGE 2 EAST OF W.M. CITY OF FERNDAL, WHATCOM COUNTY, WASHINGTON

DENSITY TABLE		
	ACRES & SQUARE FOOTAGE	PERCENTAGE
OVERALL PARCEL AREA	3.14 ACRES (136,856 SQ. FT.)	100%
RIGHT OF WAY DEDICATION	0.60 ACRES (26,101 SQ. FT.)	19.07%
TOTAL LOT AREA	2.54 ACRES (110,755 SQ. FT.)	80.93%

- LEGEND**
- ⊕ FOUND 2" BRASS DISK ROAD CENTERLINE SURFACE MONUMENT
 - ⊕ FOUND 3" BRASS DISK PLAT BOUNDARY MONUMENT IN CONCRETE PEDESTAL (P.L.S. NO. 9361)
 - ⊕ FOUND 3" ALUMINUM DISK PLAT BOUNDARY MONUMENT IN CONCRETE PEDESTAL (P.L.S. NO. 40525)
 - FOUND 1/2" REBAR WITH YELLOW CAP (P.L.S. NO. 9361)
 - ⊕ SET 2" BRASS DISK ROAD CENTERLINE SURFACE MONUMENT (P.L.S. NO. 9361)
 - ⊕ SET 3" BRASS DISK PLAT BOUNDARY MONUMENT IN CONCRETE PEDESTAL (P.L.S. NO. 9361)
 - SET #4 REBAR WITH YELLOW CAP (P.L.S. NO. 9361)
 - ⊕ CALCULATED POSITION
 - X- FENCE LINE


LINE AND CURVE TABLE			
NUMBER	LENGTH	DIRECTION OR DELTA	RADIUS
C1	38.03'	21°47'24"	100.00'
C2	30.18'	17°17'22"	100.00'
C3	30.55'	17°30'15"	100.00'
C4	34.21'	19°36'07"	100.00'
C5	25.79'	14°46'33"	100.00'
L1	24.71'	N6°04'49"E	
L2	31.85'	N39°11'22"E	
L3	19.27'	N1°58'55"E	
L4	18.00'	N88°58'46"W	

LOT CORNER NOTES


- 1 BARB WIRE FENCE IS 0.1' W. OF SET CAPPED REBAR
DEED LINE (SEE SURVEY NOTE) IS 1.16' E. OF SET CAPPED REBAR
- 2 BARB WIRE FENCE IS 0.4' E. OF SET CAPPED REBAR
DEED LINE (SEE SURVEY NOTE) IS 1.30' E. OF SET CAPPED REBAR
- 3 BARB WIRE FENCE IS 0.5' E. OF SET CAPPED REBAR
DEED LINE (SEE SURVEY NOTE) IS 1.44' E. OF SET CAPPED REBAR
- 4 BARB WIRE FENCE IS 0.3' E. OF SET CAPPED REBAR
DEED LINE (SEE SURVEY NOTE) IS 1.58' E. OF SET CAPPED REBAR
- 5 BARB WIRE FENCE IS 1.2' E. OF SET CAPPED REBAR
DEED LINE (SEE SURVEY NOTE) IS 1.71' E. OF SET CAPPED REBAR
- 6 BARB WIRE FENCE IS 0.9' E. OF SET CAPPED REBAR
DEED LINE (SEE SURVEY NOTE) IS 1.85' E. OF SET CAPPED REBAR

SURVEY NOTES:


1. THE EASTERLY PLAT BOUNDARY SHOWN HEREON WAS CREATED BY DOUGLAS PLACE LONG PLAT DIVISION 1 (AF NO. 2110101245) IN WHICH SAID EASTERLY BOUNDARY WAS ESTABLISHED BY PLATTING TO AN APPROXIMATE EXISTING FENCELINE LOCATION SHOWN ON THAT RECORD OF SURVEY FILED UNDER AUDITOR'S FILE NO. 931119056 BEING WEST OF DEED LINE ALSO SHOWN ON SAID RECORD OF SURVEY.
2. THE REVISED EAST PROPERTY LINE CREATED BY THIS PLAT SHALL DEFINE THE EAST LINE OF LOTS 1-8.

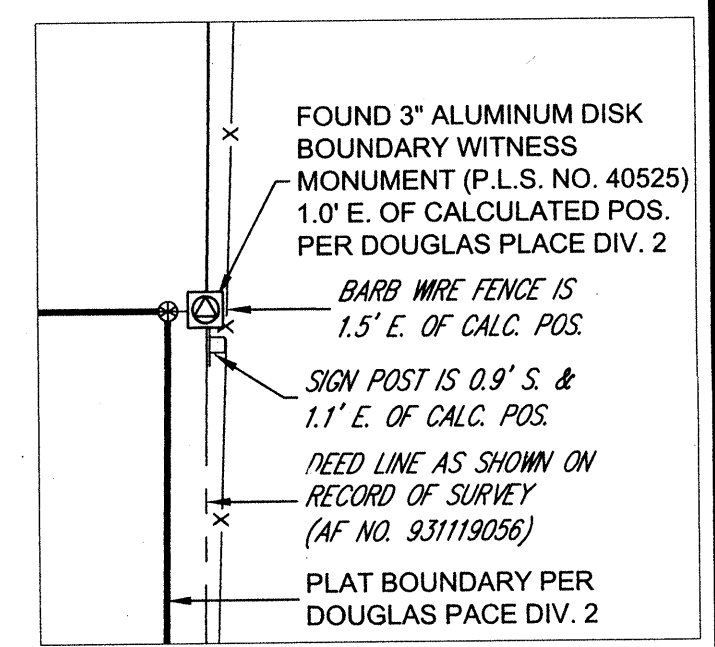

DETAIL A
(SCALE: 1" = 5')

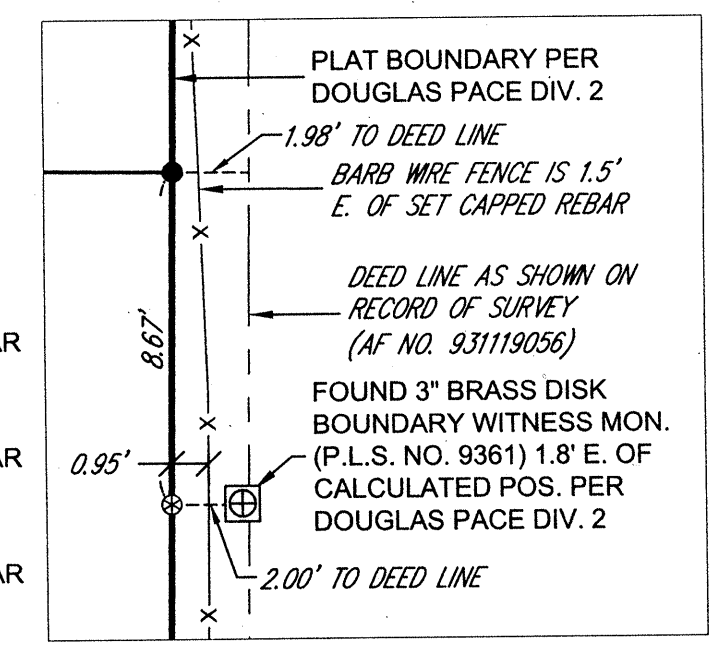

DETAIL B
(SCALE: 1" = 5')

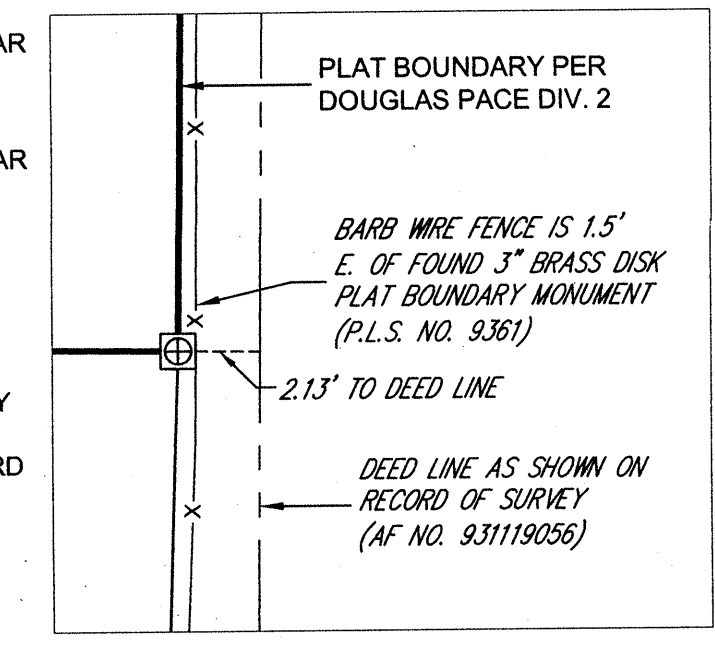

DETAIL C
(SCALE: 1" = 5')

PREPARED FOR: DOUG MARR
PTN. NW 1/4 NW 1/4 SEC. 30, TWP. 39 N., RGE. 2 E. W.M.

RONALD T. JEPSON & ASSOC.
REGISTERED PROFESSIONAL ENGINEERS AND LAND SURVEYORS
222 GRAND AVE., SUITE C, BELLINGHAM, WA 98225
PHONE: (360) 733-5760
FAX: (360) 647-8939
EMAIL: RJEPSON@JEPSONENGINEERING.COM

DOUGLAS PLACE LONG PLAT DIV. 3
PTN. NW 1/4 NW 1/4 SEC. 30, TWP. 39 N., RGE. 2 E. W.M.
CITY OF FERNDAL, WHATCOM COUNTY, WA.

JOB NO: 12082.04	ISSUE DATE: 12/15/2017	SHEET NO.: 3 of 3
DRAWN BY: DRM	CHECKED BY: RTJ	