

2120200446

Page: 1 of 2

2/03/2012 11:59 AM

PLAT \$128.00

Whatcom County, WA

Request of: SOUTH DOUGLAS LLC

PLAT

NUMBER OF SHEETS: **2**

NAME OF PLAT:

SOUTH DOUGLAS LONG PLAT DIV. 2

DECLARANTS:

SOUTH DOUGLAS LLC

BUSINESS BANK OF SKAGIT COUNTY

SURVEYOR:

RONALD T JEPSON & ASSOCIATES

SECTION: **30** TOWNSHIP: **39N** RANGE: **2E**

SOUTH DOUGLAS LONG PLAT DIV. 2

A PTN. OF THE W 1/2 OF THE NW 1/4 OF SEC. 30, TWP. 39N, R2E OF W.M.
WHATCOM COUNTY, WASHINGTON, CITY OF FERNDAL

DECLARATION AND DEDICATION

KNOW ALL MEN BY THESE PRESENTS THE UNDERSIGNED, BEING OWNERS IN FEE SIMPLE OF THE LAND HEREIN PLATTED, HEREBY DECLARE AND ACKNOWLEDGE THIS PLAT OF "SOUTH DOUGLAS LONG PLAT DIV. 2- A PLANNED RESIDENTIAL COMMUNITY" AND DEDICATE TO THE USE OF THE PUBLIC FOREVER, ALL ROADS, ALLEYS, EASEMENTS, AND PUBLIC SITES SHOWN ON THIS PLAT; ALSO, THE RIGHT TO MAKE ALL NECESSARY SLOPES FOR CUTS AND FILL UPON LOTS, BLOCKS AND TRACTS IN ANY REASONABLE GRADING OF THE ROADS, ALLEYS, EASEMENTS AND PUBLIC SITES, AND HEREBY WAIVER ALL CLAIMS FOR DAMAGES AGAINST ANY GOVERNMENTAL AUTHORITY WHICH MAY BE OCCASIONED TO ADJACENT LAND BY ESTABLISHED CONSTRUCTION, DRAINAGE, AND MAINTENANCE OF SAID ROAD.

William Kramer
SOUTH DOUGLAS LLC - A WASHINGTON LIMITED LIABILITY COMPANY
WILLIAM KRAMER - GENERAL PARTNER



BUSINESS BANK OF SKAGIT COUNTY

ACKNOWLEDGMENTS

(STATE OF WASHINGTON)
(COUNTY OF WHATCOM)

THIS IS TO CERTIFY THAT ON THE 23 DAY OF January, 2012, BEFORE ME, THE UNDERSIGNED, A NOTARY PUBLIC, HAVE PERSONALLY APPEARED William Kramer, A GENERAL PARTNER OF SOUTH DOUGLAS LLC, A WASHINGTON LIMITED LIABILITY COMPANY, TO ME KNOWN TO BE THE REPRESENTATIVES OF SAID COMPANY WHO EXECUTED THE WITHIN AND FOREGOING DEDICATION AND ACKNOWLEDGED THE SAID INSTRUMENT TO BE THE FREE AND VOLUNTARY ACT AND DEED OF SAID COMPANY FOR THE USES AND PURPOSES THEREIN MENTIONED, AND ON OATH STATED THAT HE WAS THE INDIVIDUALS AUTHORIZED TO EXECUTE THE SAID INSTRUMENT. WITNESS MY HAND AND OFFICIAL SEAL THE DAY AND YEAR FIRST MENTIONED ABOVE.

Terry A. Unger NOTARY PUBLIC IN AND FOR THE
STATE OF WASHINGTON,
RESIDING AT Bellingham

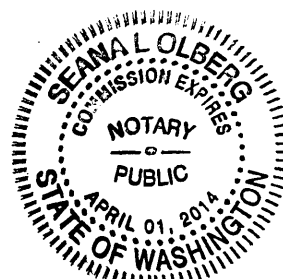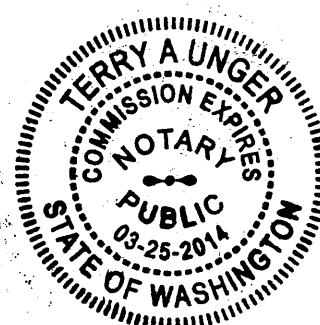

(STATE OF WASHINGTON)
(COUNTY OF WHATCOM)

THIS IS TO CERTIFY THAT ON THE 23rd DAY OF January, 2012, BEFORE ME, THE UNDERSIGNED, A NOTARY PUBLIC, HAVE PERSONALLY APPEARED John Cruikshank, A WASHINGTON CORPORATION, TO ME KNOWN TO BE THE REPRESENTATIVES OF SAID COMPANY WHO EXECUTED THE WITHIN AND FOREGOING DEDICATION AND ACKNOWLEDGED THE SAID INSTRUMENT TO BE THE FREE AND VOLUNTARY ACT AND DEED OF SAID COMPANY FOR THE USES AND PURPOSES THEREIN MENTIONED, AND ON OATH STATED THAT THEY HE/SHE WAS INDIVIDUAL AUTHORIZED TO EXECUTE THE SAID INSTRUMENT. WITNESS MY HAND AND OFFICIAL SEAL THE DAY AND YEAR FIRST MENTIONED ABOVE.

Seema L. Olberg NOTARY PUBLIC IN AND FOR THE
STATE OF WASHINGTON,
RESIDING AT Bellingham

NOTES

- ONE-HALF OF THE TRAFFIC MITIGATION FEE MUST BE PAID AT TIME OF ISSUANCE OF BUILDING PERMIT.
- WATER AND SEWER CONNECTION FEES MUST BE PAID AT TIME OF ISSUANCE OF BUILDING PERMIT.
- ONE-HALF OF THE PARK IMPACT FEE MUST BE PAID AT TIME OF ISSUANCE OF BUILDING PERMIT.
- SCHOOL IMPACT FEES WILL BE PAID IN ACCORDANCE WITH THE REQUIREMENTS OF THE FERNDAL SCHOOL DISTRICT.
- EASEMENT NOTE: A 5' UTILITY EASEMENT SHALL BE MAINTAINED AROUND THE PERIMETER OF ALL LOTS PER CITY OF FERNDAL STANDARDS AND 10' UTILITY EASEMENT IS ADOPTED OVER THE FRONT OF ALL LOTS STREET FRONTAGE.
- ALL UTILITY, DRAINAGE, AND ACCESS EASEMENTS SHALL BE WRITTEN IN FAVOR OF THE CITY OF FERNDAL IN ADDITION TO THE OTHER PARTIES REFERENCED.
- THE SOUTHWEST SEWER BYPASS FEE MUST BE PAID AT TIME OF ISSUANCE OF BUILDING PERMIT.
- AS IS UNDETERMINED, THERE IS EXISTING FILL ON SOME OF THE LOTS WITHIN THIS SUBDIVISION THAT WILL REQUIRE GEOTECHNICAL TESTING TO DETERMINE WHETHER OR NOT FUTURE FOUNDATION ENVELOPES ARE LOCATED ON "LOAD-BEARING" SOIL. A GEOTECHNICAL REPORT SHALL BE SUBMITTED FOR EVERY SINGLE-FAMILY BUILDING PERMIT APPLICATION THAT ADDRESSES THE STABILITY OF THE UNDERLYING SOIL.
- ANY DISTURBANCE TO THE WETLANDS INDICATED ON LOTS 20, 23, AND 24 THAT WERE DELINEATED PER THE MARCH 8TH 2006 "FISHER-DOUGLAS ROAD, WETLAND RECONNAISSANCE AND DELINEATION" BY ATSI SHALL CONFORM TO THE CITY OF FERNDAL CRITICAL AREAS ORDINANCE.

LEGAL DESCRIPTION

TRACT 4 OF SOUTH DOUGLAS LONG PLAT DIVISION 1
FILED UNDER AF#2090102033, RECORDS OF THE
WHATCOM COUNTY AUDITOR.

COVENANTS, CONDITIONS, RESERVATIONS AND RESTRICTIONS

THESE COVENANTS SHALL RUN WITH THE LAND AND SHALL BE REFERENCED ON ANY CONVEYANCES OR AGREEMENTS OF USAGE FOR THE LOTS SHOWN. FILED UNDER AF#2111200745 AND AF# 2120200447

RECIPROCAL STORMWATER FACILITY EASEMENT

ACCESS TO STORMWATER FACILITIES TO REMAIN UNOBSTRUCTED FOR INSPECTION AND MAINTENANCE OF THE SYSTEM. ACCESS ROADS ARE TO BE MAINTAINED FOR VEHICLE ACCESS. NO ALTERATION IS ALLOWED WITHOUT PRIOR CITY OF FERNDAL APPROVAL. SUBJECT TO AF#2111200745.

PLAT ADMINISTRATOR'S APPROVAL

EXAMINED AND APPROVED BY THE PLAT ADMINISTRATOR OF FERNDAL
THIS 2nd DAY OF February, 2012

[Signature]
PLAT ADMINISTRATOR, FERNDAL, WASHINGTON

PUBLIC WORKS DIRECTOR'S APPROVAL

EXAMINED AND APPROVED BY THE CITY OF FERNDAL DEPARTMENT OF PUBLIC WORKS
THIS 2nd DAY OF February, 2012

[Signature] P.E.
DIRECTOR OF PUBLIC WORKS, FERNDAL, WASHINGTON

CITY CLERK'S APPROVAL

EXAMINED AND APPROVED BY THE FERNDAL CITY CLERK,
THIS 2nd DAY OF January, 2012

[Signature]
CITY CLERK, CITY OF FERNDAL, WASHINGTON

MAINTENANCE AGREEMENT

ALL COSTS OF MAINTAINING, REPAIRING, IMPROVING OR COST OTHERWISE CONNECTED WITH ANY STORMWATER FACILITY, DESIGNATED WETLAND, OPEN SPACE TRACT, OR OTHER COMMON FACILITIES OR OPEN SPACE ELEMENTS SHALL BE BORN BY THE HOMEOWNER'S ASSOCIATION ACCORDING TO THE COVENANTS, CONDITIONS, RESERVATIONS, AND RESTRICTIONS(CC&R'S) OF THE PLAT SOUTH DOUGLAS LONG PLAT DIV. 1, AS RECORDED UNDER A.F.#2090102034, AUDITOR'S OFFICE, WHATCOM COUNTY, WASHINGTON.

COUNTY TREASURER'S CERTIFICATE

I, STEVE OLIVER, TREASURER OF WHATCOM COUNTY, DO HEREBY CERTIFY THAT ALL TAXES REQUIRED BY LAW TO BE PAID UPON THAT PORTION OF REAL ESTATE EMBRACED WITHIN THIS PLAT OF "SOUTH DOUGLAS LONG PLAT DIV. 2 - A PLANNED RESIDENTIAL COMMUNITY" AND ALL DELINQUENT ASSESSMENTS HAVE BEEN FULLY PAID AS SHOWN IN THE RECORDS OF MY OFFICE THIS 3rd DAY OF February, 2012


Steve N. Oliver - March 1st 2012 Deputy Treasurer
STEVE OLIVER TREASURER, WHATCOM COUNTY, WASHINGTON



LAND SURVEYOR CERTIFICATION

I HEREBY CERTIFY THAT "SOUTH DOUGLAS LONG PLAT DIV. 2 - A PLANNED RESIDENTIAL COMMUNITY" LONG PLAT WAS PREPARED UNDER MY DIRECTION, AND IS BASED UPON AN ACTUAL FIELD SURVEY AT THE REQUEST OF BILL KRAMER AUGUST, 2011; THAT THE TECHNICAL DATA IS CORRECTLY SHOWN THEREON, AND THAT ALL REQUIRED MONUMENTS AND/OR PARCEL CORNER MARKERS ARE SET.

Ronald T. Jepson P.E., P.L.S.
RONALD T. JEPSON L.S. NO. 9361

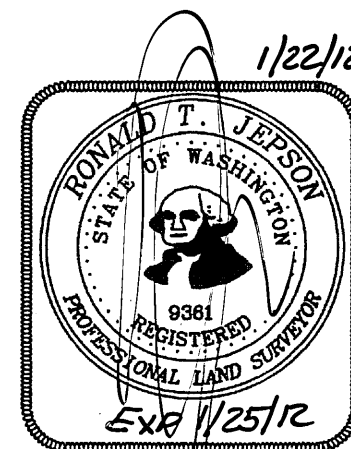


AUDITOR'S CERTIFICATE

I HEREBY CERTIFY THAT THIS SHORT PLAT WAS FILED FOR RECORD IN THE OFFICE OF THE AUDITOR OF WHATCOM COUNTY, WASHINGTON THIS 3rd DAY OF February, 2012 AT 11:59 A.M./P.M. AT THE REQUEST OF Ronald T. Jepson Assoc. AND IS RECORDED UNDER AUDITOR'S FILE

NUMBER 2120200446

Debbie Kellerman
AUDITOR OF WHATCOM COUNTY BY

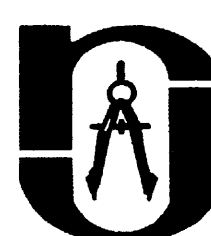



RONALD T. JEPSON & ASSOCIATES

REGISTERED PROFESSIONAL ENGINEERS AND LAND SURVEYORS 222 GRAND AVE., SUITE C, BELLINGHAM, WASHINGTON 98225 PH.(360)733-5760 FAX (360)647-8939 EMAIL: RJEPSON@JEPSONENGINEERING.COM


2120200446

SOUTH DOUGLAS LONG PLAT DIV. 2


A PTN. OF THE W 1/2 OF THE NW 1/4 OF SEC. 30, TWP. 39N, R2E OF W.M.
WHATCOM COUNTY, WASHINGTON, CITY OF FERNDAL

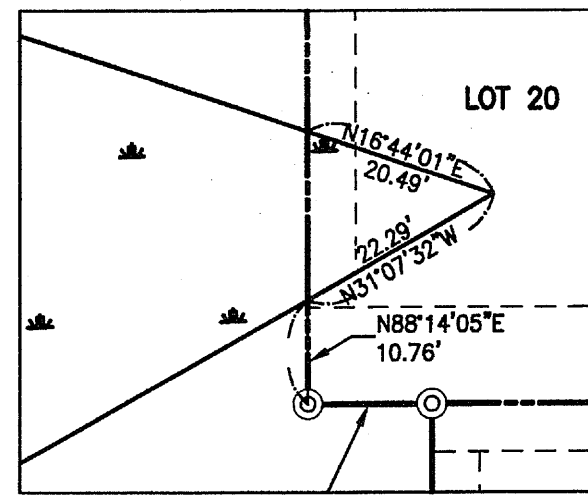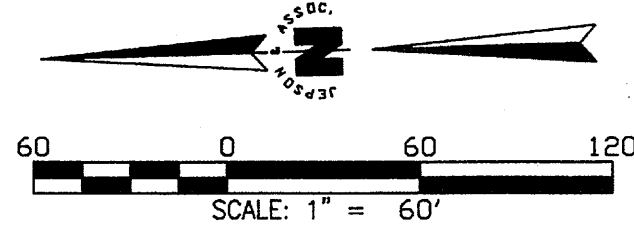

WETLAND DETAIL "A"

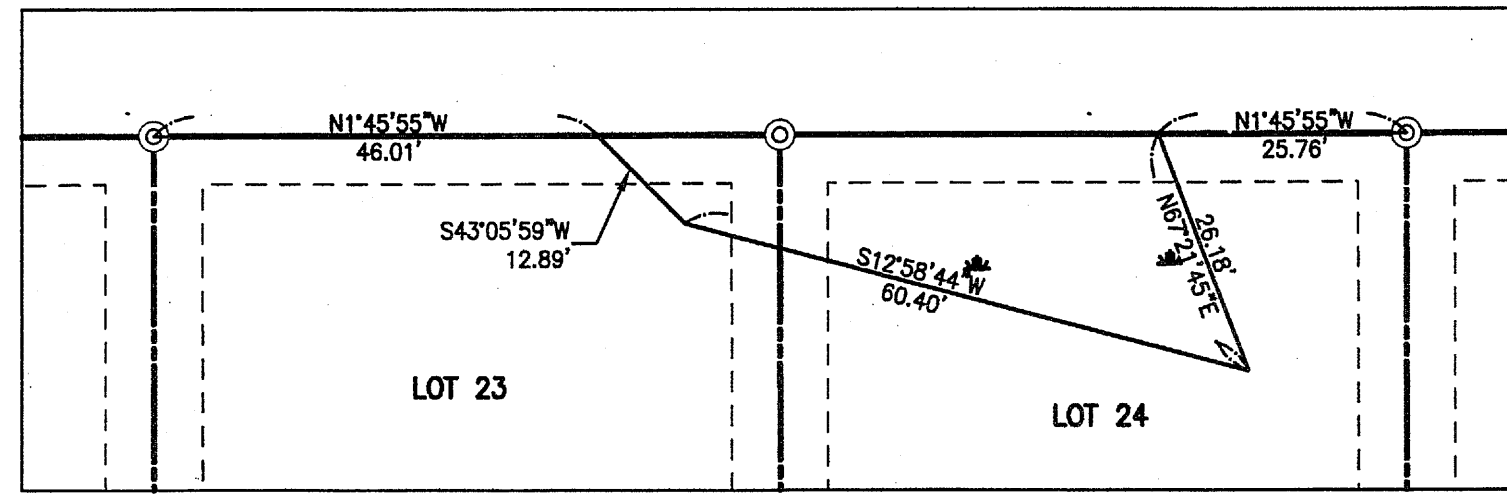

WETLAND DETAIL "B"

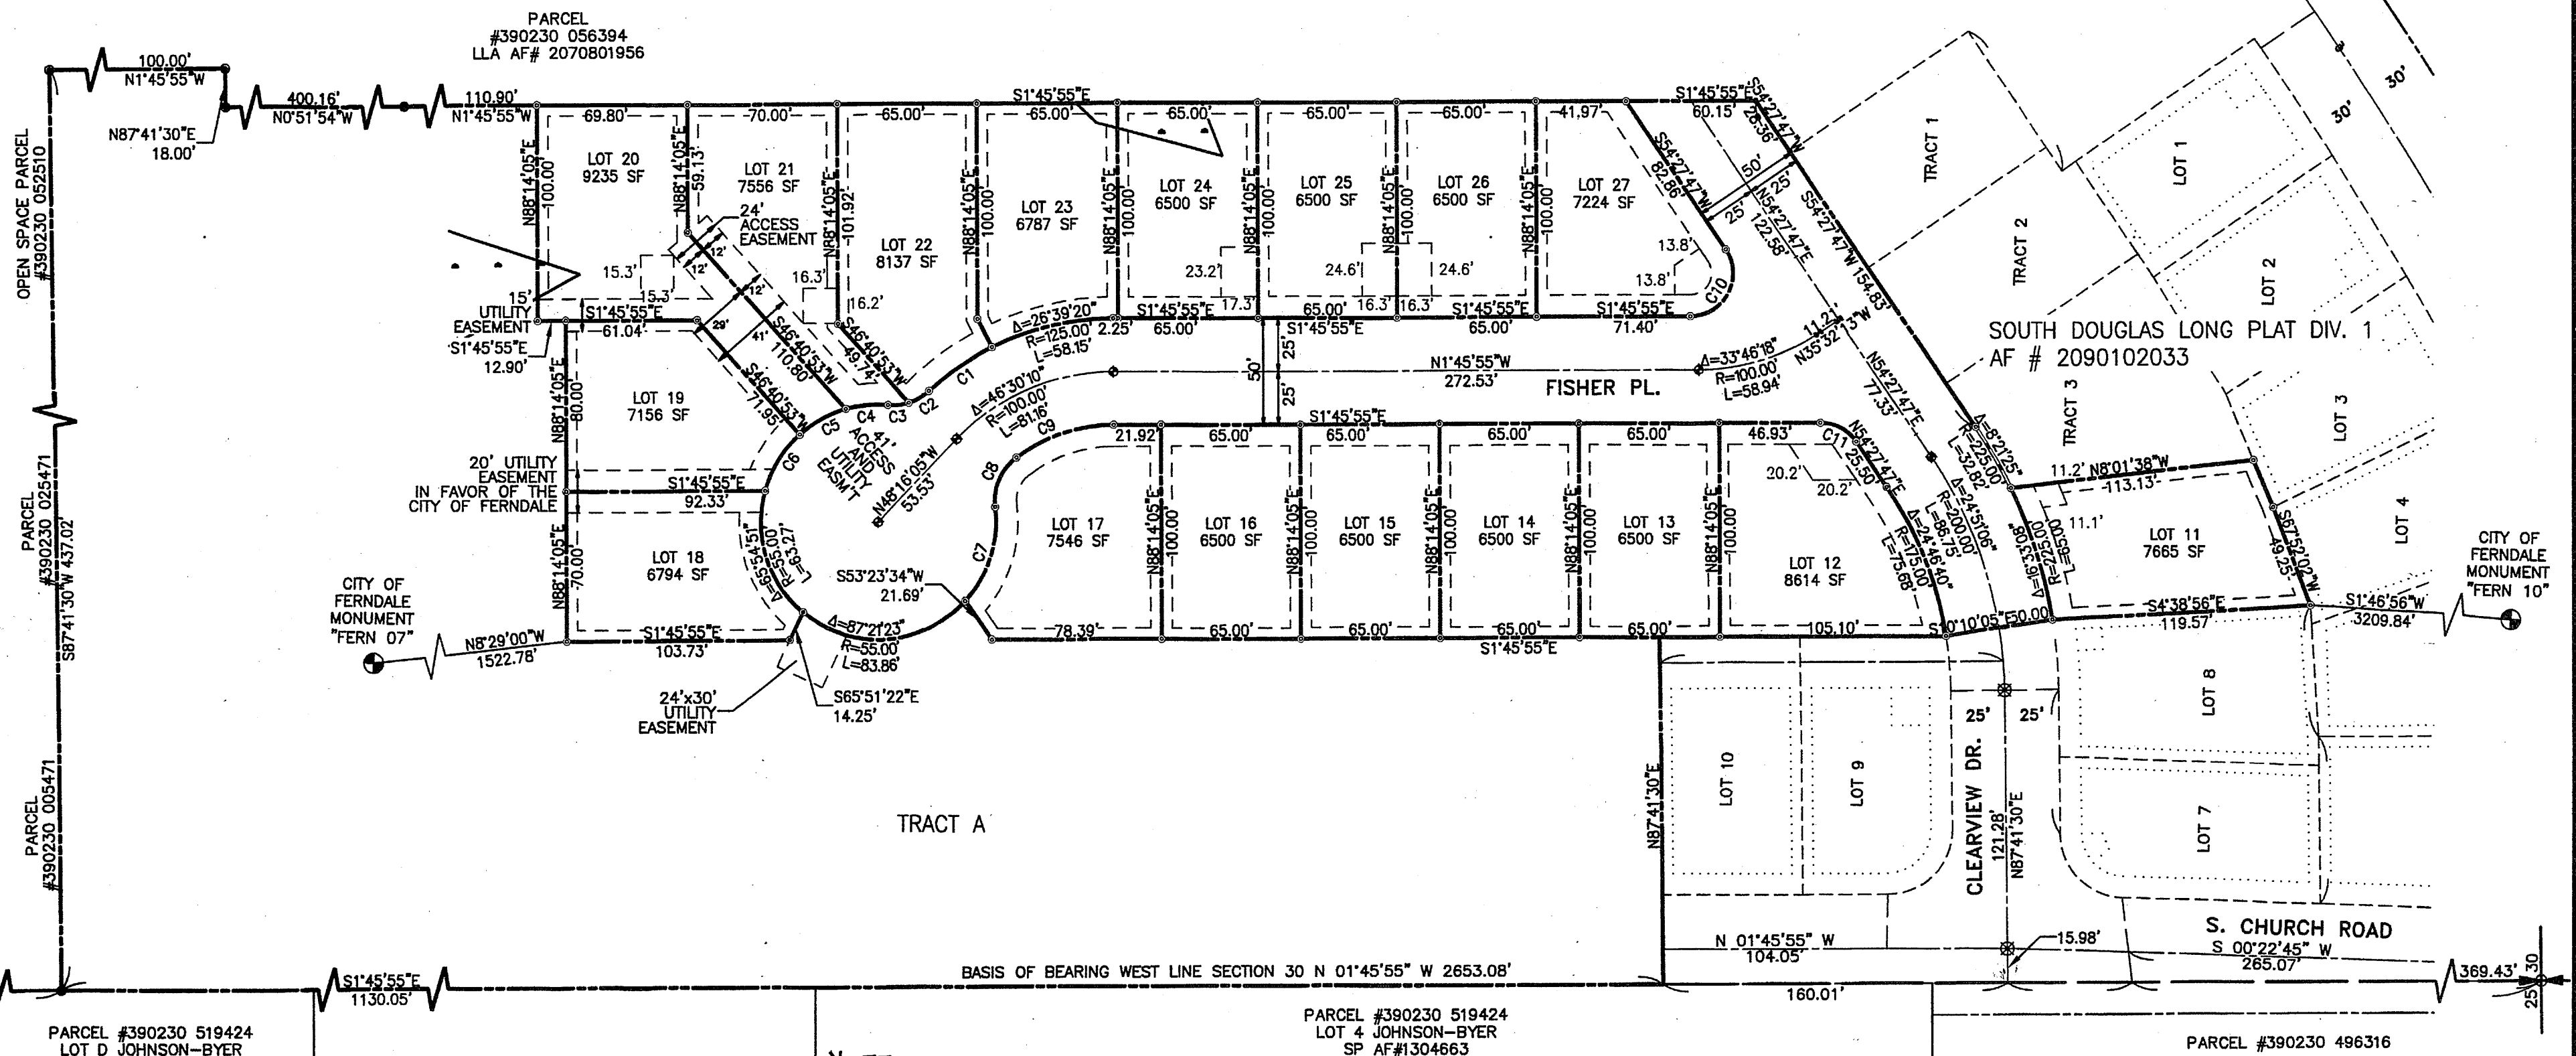

LEGEND

- SET REBAR & CAP #9361
- ✚ FOUND SECTION CORNER
- ✚ FOUND 1/4 SEC CORNER
- SET BRASS DISK
- ✚ FOUND BRASS DISK FROM PHASE 1

BASIS OF BEARING

THAT RECORD OF SURVEY FILED UNDER WHATCOM COUNTY AF #931119056
BEARING BEING N 01°45'55" W WEST LINE OF SECTION 30

DATUM

HORIZONTAL: NAD 83/91
VERTICAL: NGVD 29

SURVEY EQUIPMENT & PROCEDURE

THIS SURVEY WAS COMPLETED AND ACCOMPLISHED BY FIELD TRAVERSE USING A
NIKON DTM-521 TOTAL STATION IN JAN 2008.



NOTE

SEE COVENANT AND RESTRICTIONS FILED UNDER AF#2090102034
AND AF #2120200447 FOR DETAILS AND CONSTRUCTION OF
RAIN GARDENS.

CURVE TABLE			
CURVE #	LENGTH	RADIUS	DELTA
C1	35.68'	125.00'	Δ016°21'12"
C2	11.09'	25.00'	Δ025°24'22"
C3	9.89'	25.00'	Δ022°40'24"
C4	19.92'	55.00'	Δ020°45'05"
C5	24.84'	55.00'	Δ025°52'20"
C6	31.31'	55.00'	Δ032°37'12"
C7	47.74'	55.00'	Δ049°43'42"
C8	26.30'	25.00'	Δ060°17'03"
C9	48.29'	75.00'	Δ036°53'21"
C10	43.20'	20.00'	Δ123°46'18"
C11	19.63'	20.00'	Δ056°13'42"

LOTS		
LOT #	AREA	ADDRESS
11	7665 SF	2467 Clearview Drive
12	8614 SF	5533 Fisher Place
13	6500 SF	5537 Fisher Place
14	6500 SF	5541 Fisher Place
15	6500 SF	5545 Fisher Place
16	6500 SF	5549 Fisher Place
17	7546 SF	5553 Fisher Place
18	6794 SF	5567 Fisher Place
19	7156 SF	5570 Fisher Place
20	9235 SF	5566 Fisher Place
21	7556 SF	5562 Fisher Place
22	8137 SF	5558 Fisher Place
23	6787 SF	5554 Fisher Place
24	6500 SF	5550 Fisher Place
25	6500 SF	5546 Fisher Place
26	6500 SF	5542 Fisher Place
27	7224 SF	5538 Fisher Place

RAINGARDENS	
LOT #	AREA
11	222 SF
12	311 SF
20	229 SF
21	264 SF
24	400 SF
25	400 SF
26	400 SF
27	272 SF

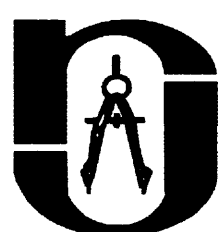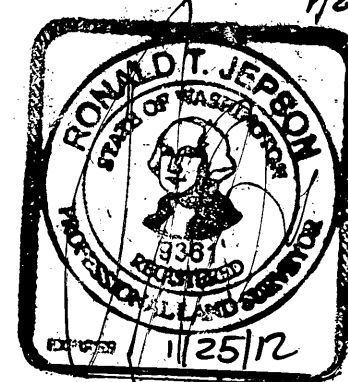

RONALD T. JEPSON & ASSOCIATES

REGISTERED PROFESSIONAL ENGINEERS AND LAND SURVEYORS 222 GRAND AVE., SUITE C, BELLINGHAM, WASHINGTON 98225 PH.(360)733-5760 FAX (360)647-8939 EMAIL: RJEPSON@JEPSONENGINEERING.COM

05055

2
OF 2