



2150201460

Page: 1 of 3

2/12/2015 3:55 PM

PLAT \$138.00

Whatcom County, WA

Request of: SOUTH DOUGLAS LLC

PLAT

NUMBER OF SHEETS: **3**

NAME OF PLAT:

SOUTH DOUGLAS LONG PLAT DIVISION 3

DECLARANTS:

SOUTH DOUGLAS LLC

WILLIAM KRAMER


SURVEYOR:

SOUTH DOUGLAS LLC

SECTION: **30** TOWNSHIP: **39N** RANGE: **2E**

2150201460

SOUTH DOUGLAS LONG PLAT DIVISION 3
A PORTION OF THE NW 1/4 OF SECTION 30
TOWNSHIP 39 N., RANGE 2 E. OF THE W.M.
CITY OF FERNDALE, WHATCOM COUNTY, WASHINGTON

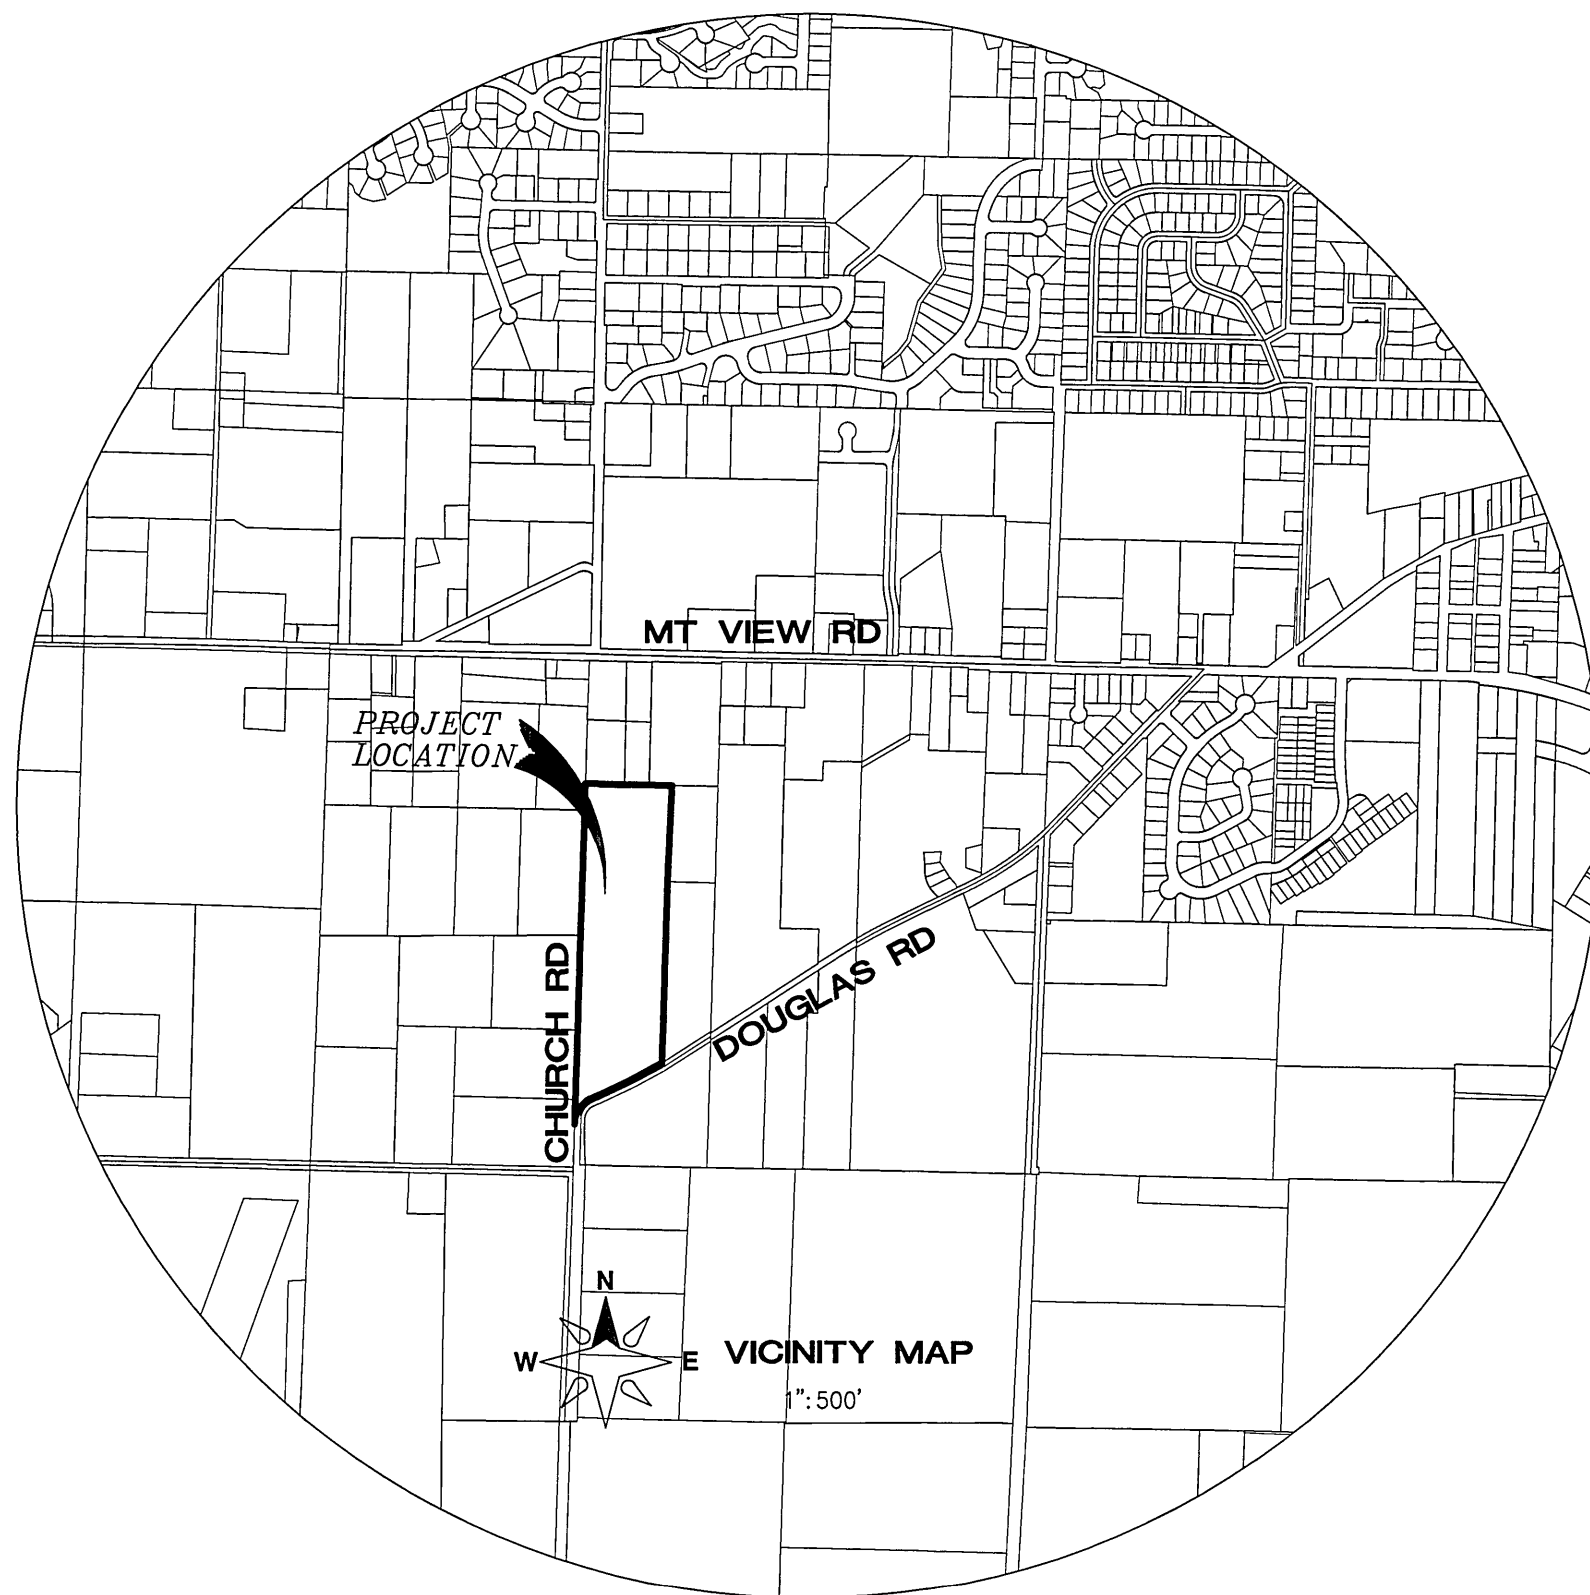

LEGAL DESCRIPTION:
(PER FIRST AMERICAN TITLE INSURANCE COMPANY ORDER No. 2352001)

TRACT A, SOUTH DOUGLAS LONG PLAT, DIVISION 2, ACCORDING TO THE PLAT THEREOF, RECORDED FEBRUARY 03, 2012, UNDER WHATCOM COUNTY AUDITOR'S FILE NUMBER 2120200446, RECORDS OF WHATCOM COUNTY, WASHINGTON, AND AS AMENDED UNDER WHATCOM COUNTY AUDITOR'S FILE NUMBER 2121003585, SITUATE IN WHATCOM COUNTY, WASHINGTON

DECLARATION & DEDICATION:

THE UNDERSIGNED OWNER(S), HEREBY DECLARE THIS LONG PLAT AND DEDICATE TO THE USE OF THE PUBLIC FOREVER THE ROAD RIGHT-OF-WAYS; AND HEREBY WAIVER ALL CLAIMS FOR DAMAGES AGAINST ANY GOVERNMENTAL AUTHORITY WHICH MAY BE OCCASIONED TO ADJACENT LAND BY THE ESTABLISHED CONSTRUCTION, DRAINAGE AND MAINTENANCE OF SAID ROAD, AND MADE WITH OUR FREE CONSENT AND IN ACCORDANCE WITH OUR WISHES.

William Kramer
WILLIAM KRAMER
SOUTH DOUGLAS, LLC, A WASHINGTON LIMITED LIABILITY COMPANY

ACKNOWLEDGMENT

STATE OF WASHINGTON)
COUNTY OF WHATCOM) SS


ON THIS 6th DAY OF FEBRUARY, 2015, BEFORE ME PERSONALLY APPEARED WILLIAM KRAMER, TO ME KNOWN TO BE A GENERAL PARTNER OF THE LIMITED LIABILITY COMPANY THAT EXECUTED THE WITHIN AND FOREGOING INSTRUMENT TO BE THE FREE AND VOLUNTARY ACT AND DEED OF SAID LIMITED PARTNERSHIP FOR THE USES AND PURPOSES THEREIN MENTIONED, AND ON OATH STATED THAT HE WAS AUTHORIZED TO EXECUTE SAID INSTRUMENT.

IN WITNESS WHEREOF, I HAVE HEREUNTO SET MY HAND AND OFFICIAL SEAL THE DAY AND YEAR FIRST ABOVE WRITTEN.

Sergio Ruiz
NOTARY PUBLIC IN AND FOR THE STATE OF WASHINGTON

RESIDING IN LYNDEN

MY COMMISSION EXPIRES: JULY 27, 2018

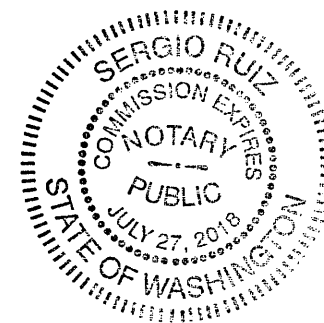

PUBLIC WORKS DIRECTOR'S APPROVAL

EXAMINED AND APPROVED BY THE CITY OF FERNDALE DEPARTMENT OF PUBLIC WORKS AS TO THE SURVEY DATA, LAYOUT OF ROADS & AND OTHER RIGHT-OF-WAYS
THIS 10 DAY OF FEBRUARY, 2015

[Signature]
PUBLIC WORKS DIRECTOR, CITY OF FERNDALE, WASHINGTON

PLAT ADMINISTRATOR APPROVAL

EXAMINED AND APPROVED BY THE CITY OF FERNDALE PLAT ADMINISTRATOR THIS 9th DAY OF FEBRUARY, 2015

[Signature]
PLAT ADMINISTRATOR, CITY OF FERNDALE, WASHINGTON

CITY CLERK'S APPROVAL

THIS PLAT APPROVED AND ROADS ACCEPTED BY ORDER OF THE CITY CLERK OF FERNDALE, WASHINGTON, THIS 9th DAY OF FEBRUARY, 2015

[Signature]
CITY CLERK, CITY OF FERNDALE, WASHINGTON

COUNTY TREASURER'S CERTIFICATE

I Steven H. Oliver, TREASURER OF WHATCOM COUNTY, WASHINGTON, DO HEREBY CERTIFY THAT ALL TAXES REQUIRED BY LAW TO BE PAID UPON THE REAL ESTATE EMBRACED WITHIN THIS PLAT OF "SOUTH DOUGLAS LONG PLAT DIVISION 3" AND ALL THE DELINQUENT ASSESSMENTS HAVE BEEN FULLY PAID. AS SHOWN IN THE RECORDS OF MY OFFICE, THIS 12th DAY OF FEBRUARY, 2015

Nicki Moore
TREASURER, WHATCOM COUNTY, WASHINGTON



CCR'S

THESE COVENANTS SHALL RUN WITH THE LAND AND SHALL BE REFERENCED ON ANY CONVEYANCES OR AGREEMENTS OF USAGE FOR THE LOTS SHOWN, FILED UNDER AF# 2150201461

STORMWATER FACILITY EASEMENT

ACCESS TO STORMWATER FACILITIES TO REMAIN UNOBSTRUCTED FOR INSPECTION AND MAINTENANCE OF THE SYSTEM, ACCESS ROADS ARE TO BE MAINTAINED FOR VEHICLE ACCESS. NO ALTERATION IS ALLOWED WITHOUT PRIOR CITY OF FERNDALE APPROVAL.

MAINTENANCE AGREEMENT

ALL COSTS OF MAINTAINING, REPAIRING, IMPROVING OR COST OTHERWISE CONNECTED WITH ANY STORMWATER FACILITY, DESIGNATED WETLAND, OPEN SPACE TRACT, OR OTHER COMMON FACILITIES OR OPEN ELEMENTS SHALL BE BORNE BY THE HOMEOWNER'S ASSOCIATION ACCORDING TO THE COVENANTS, CONDITIONS, RESERVATIONS AND RESTRICTIONS (CC&R'S) OF THE PLAT SOUTH DOUGLAS LONG PLAT DIVISION 3, AS RECORDED UNDER AF# 2150201461 IN THE CITY CLERK'S OFFICE, WHATCOM COUNTY, WASHINGTON.

CITY NOTES:

- ONE HALF OF TRAFFIC, PARK AND SCHOOL MITIGATION FEES HAVE BEEN PAID, THE REMAINING HALF SHALL BE PAID PURSUANT TO BUILDING PERMIT CONDITIONS APPROVAL. THE SOUTHWEST SEWER BYPASS FEE, WATER AND SEWER CONNECTION FEES SHALL BE PAID PURSUANT TO BUILDING PERMIT CONDITIONS OF APPROVAL.
- STORM SEWER MITIGATION FEES HAVE BEEN PAID PER SQUARE FOOT OF GROSS PROPERTY AREA.

ACCESS AND UTILITY EASEMENT

THE ACCESS & UTILITY EASEMENT ESTABLISHED ON THE FACE OF THIS PLAT SHALL BE GOVERNED BY THE TERMS AND CONDITIONS OF THE 24' ACCESS & UTILITY EASEMENT SET FORTH IN THE SOUTH DOUGLAS LONG PLAT, DIV.1 (RECORDED AT WHATCOM COUNTY AUDITOR'S FILE NUMBER 2090102033) AND THE DECLARATION OF COVENANTS, CONDITIONS, RESERVATION AND RESTRICTIONS OF THE SOUTH DOUGLAS LONG PLAT, DIV. 1 (RECORDED AT WHATCOM COUNTY AUDITOR'S FILE NUMBER 2090102034).

SURVEY NOTES:

- DATA FOR THIS SURVEY WAS GATHERED BY FIELD TRAVERSE UTILIZING ELECTRONIC DATA COLLECTION.
- EQUIPMENT USED: LEICA TCRA1103+; 00'01.5" ± 2 PPM, ± 2 MM
- HORIZONTAL DATUM: WASHINGTON STATE NORTH ZONE NAD 83/91. CITY OF FERNDALE "SURVEY MONUMENT NETWORK" MONUMENT NUMBER 7
- PER TITLE REPORT, EASEMENT NOT AFFECTING SUBJECT PARCEL: AF# 2071002258

AUDITOR'S CERTIFICATE

Filed for record this 12 day of Feb 2015, at 3:55p
in official records under Auditor's File Number.

2150201460


at the request of South Douglas LLC
Debbie Adelman by Kelli Whelan
County Auditor

SURVEYOR'S CERTIFICATE

This map correctly represents a survey made by me or under my direction in conformance with the requirements of the Survey Recording Act at the request of WILLIAM KRAMER

in FEB 20 15

Certificate No.: 24218

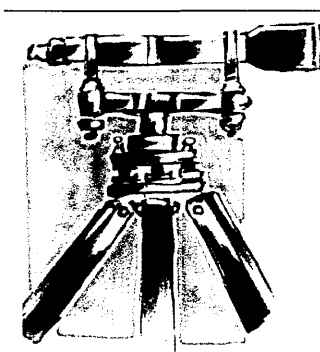

LAND DEVELOPMENT
ENGINEERING & SURVEYING INC.


5160 INDUSTRIAL PL. #108
FERNDAL, WA 98248
Ph (360) 383-0620

LONG PLAT FOR:
SOUTH DOUGLAS, LLC

JOB No. 13011	DWG No. 13011-PLAT.dwg	DATE: 02/04/15
DRN BY: SR	CHK BY: K.T.H.	SHEET 1 of 3

2150201460


SOUTH DOUGLAS LONG PLAT DIVISION 3
A PORTION OF THE NW 1/4 OF SECTION 30
TOWNSHIP 39 N., RANGE 2 E. OF THE W.M.
CITY OF FERNDALE, WHATCOM COUNTY, WASHINGTON

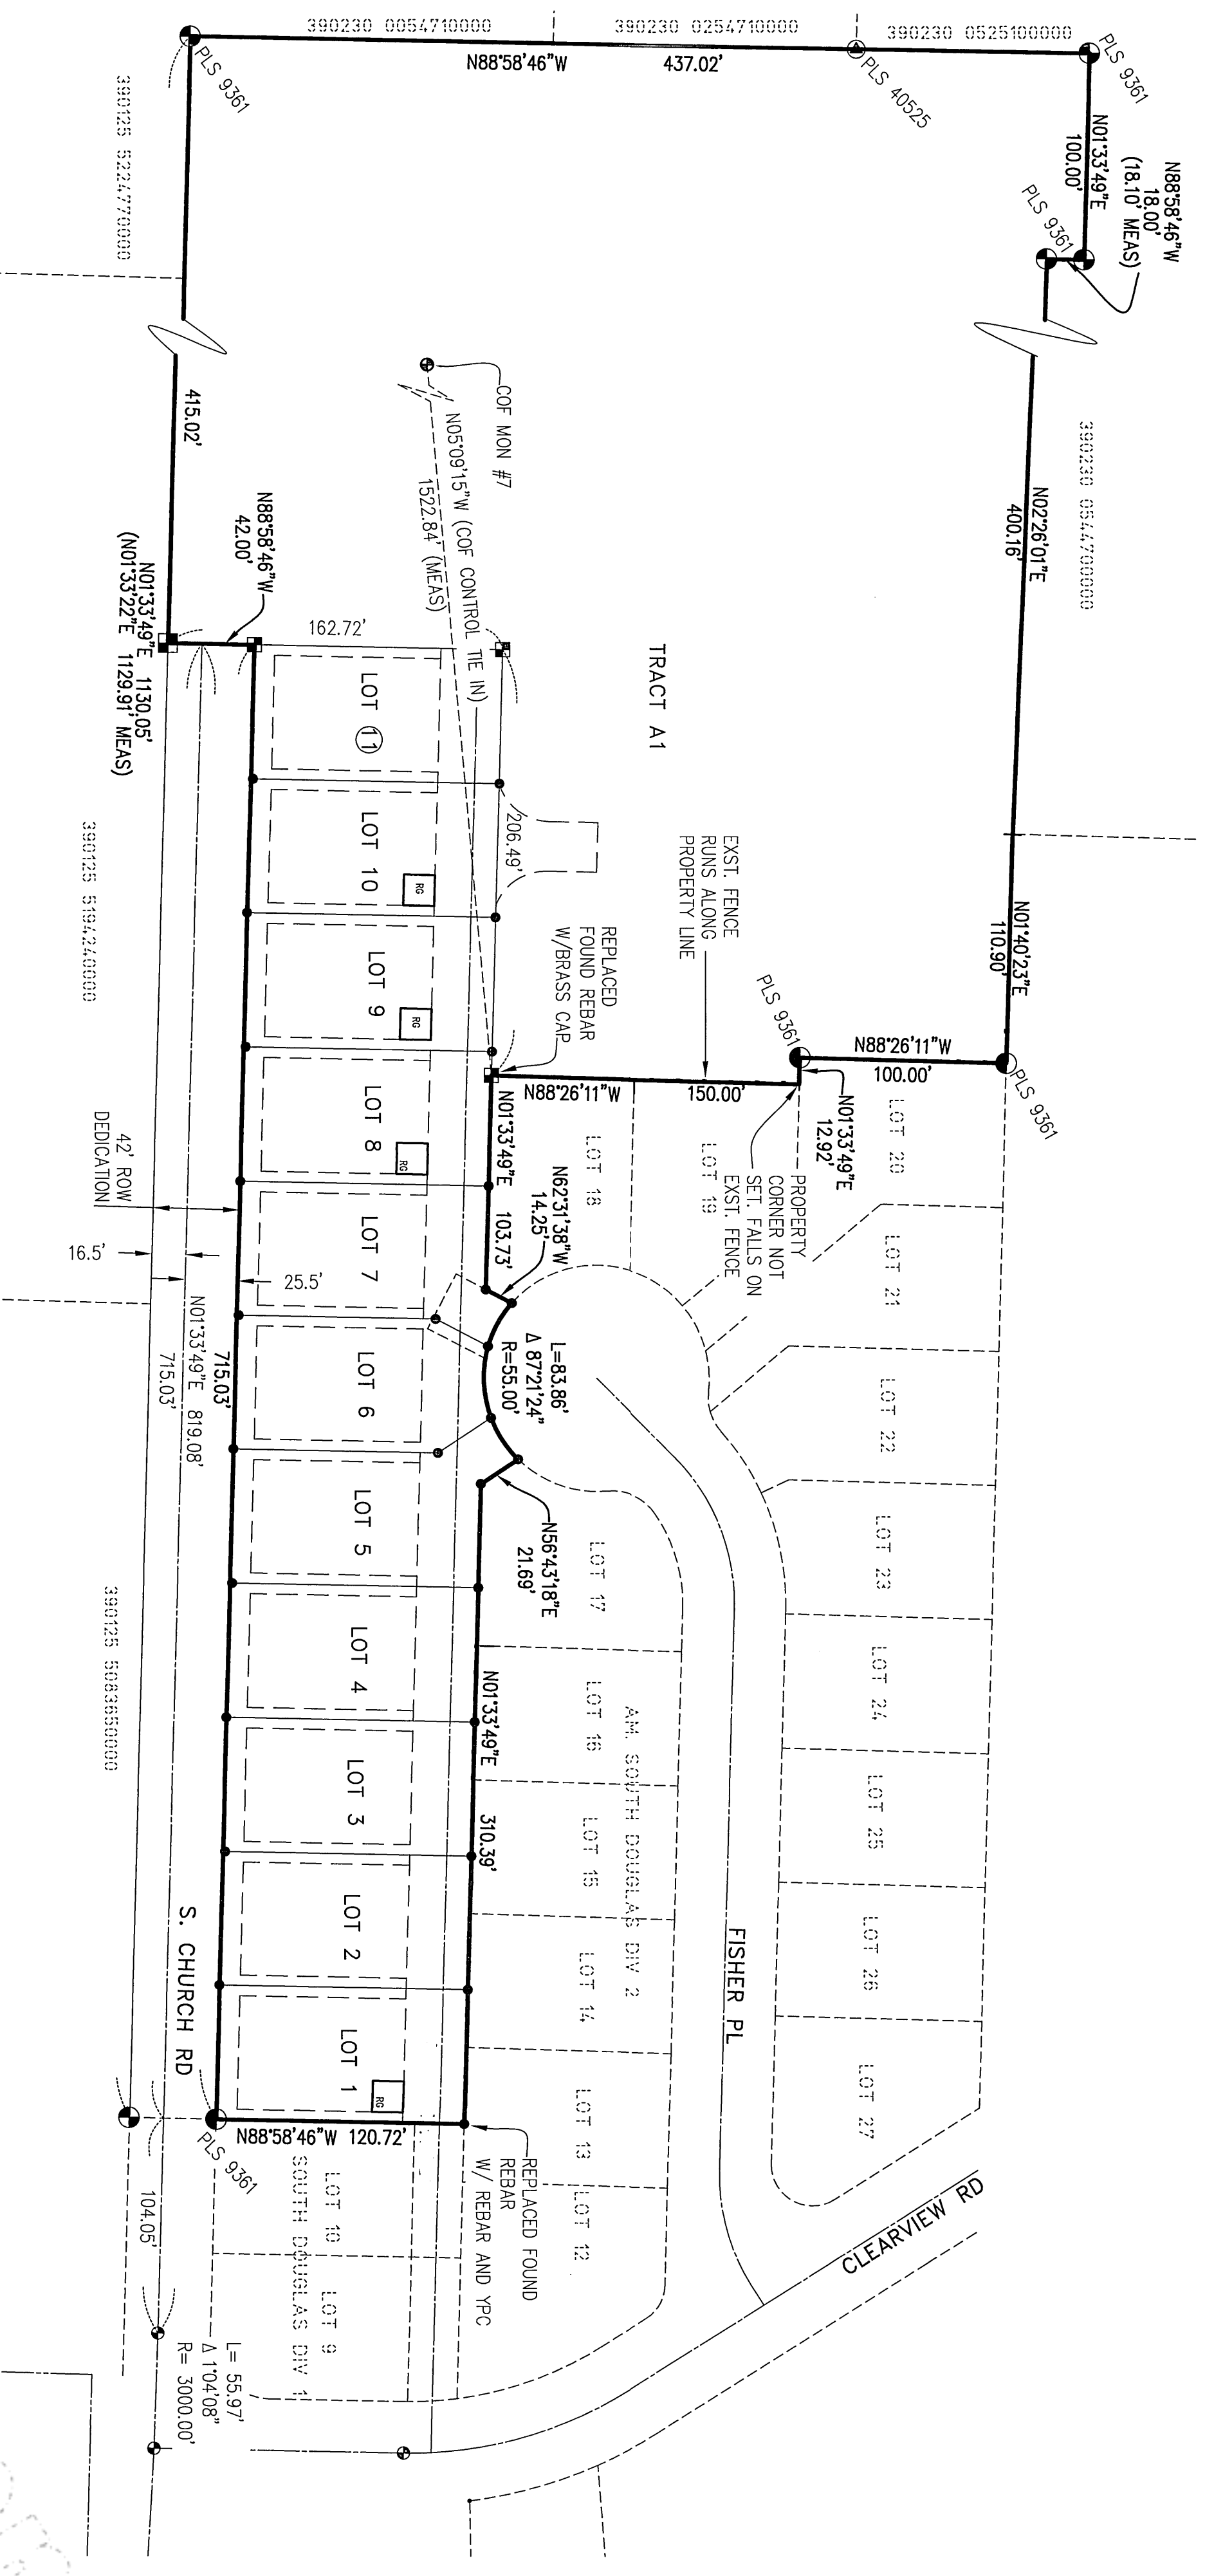

LEGEND:

- = FND BRASS MON (APRIL 2013)
 ● = FND ALUMINUM CAP MON (APRIL 2013)
 = SET 3" BRASS CAP MON MARKED
 "LDES INC 24218", NOV. 2014
 ■
 ● = FUND REBAR W/YELLOW PLASTIC CAP
 MARKED "JEPSON 9361", NOV. 2014
 ● = SET REBAR W/YELLOW PLASTIC CAP
 MARKED "LDES INC 24218", NOV. 2014
 = LOT ADDRESS

RG = RAIN GARDEN LOCATION

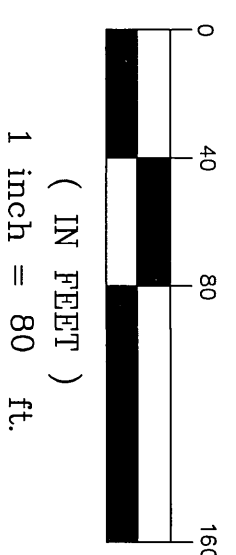

(IN FEET)
1 inch = 80 ft.

RAIN GARDEN


LOT 1:

INFILTRATION RATE= 0.50 IN/HR
RG SIZE= 225SF; GRAVEL DEPTH= 2'
RISER ELEV.= 51.67

LOT 8-9: INFLATION RATE - N/A

INFILTRATION RATE= N/A
RG SIZE= 225SF; GRAVEL DEPTH= 2'
RISER ELEV.= 57.62 (LOT 8)
RISER ELEV.= 59.60 (LOT 9)

L01 10:
INFILTRATION RATE= 0.50 IN/HR
RG SIZE= 225SF; GRAVEL DEPTH= 2'
RISER ELEV.= 62.00

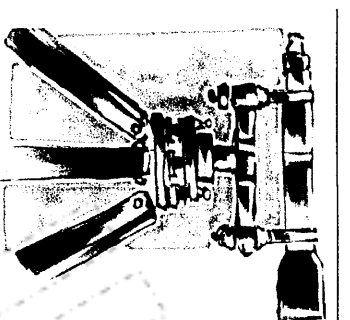


LAND DEVELOPMENT
ENGINEERING & SURVEYING INC.
5160 INDUSTRIAL PL. #108
FERNDALE, WA 98248
Ph (360) 383-0620

LONG PLAT FOR:
SOUTH DOUGLAS, LLC

JOB No. 13011	DWG No. 13011-PLAT.dwg	DATE: 02/04/15
DRN BY: SR	CHK BY: K.T.H.	SHEET 2 of 3

2150201460

SOUTH DOUGLAS LONG PLAT DIVISION 3
A PORTION OF THE NW 1/4 OF SECTION 30
TOWNSHIP 39 N., RANGE 2 E. OF THE W.M.
CITY OF FERNDALE, WHATCOM COUNTY, WASHINGTON


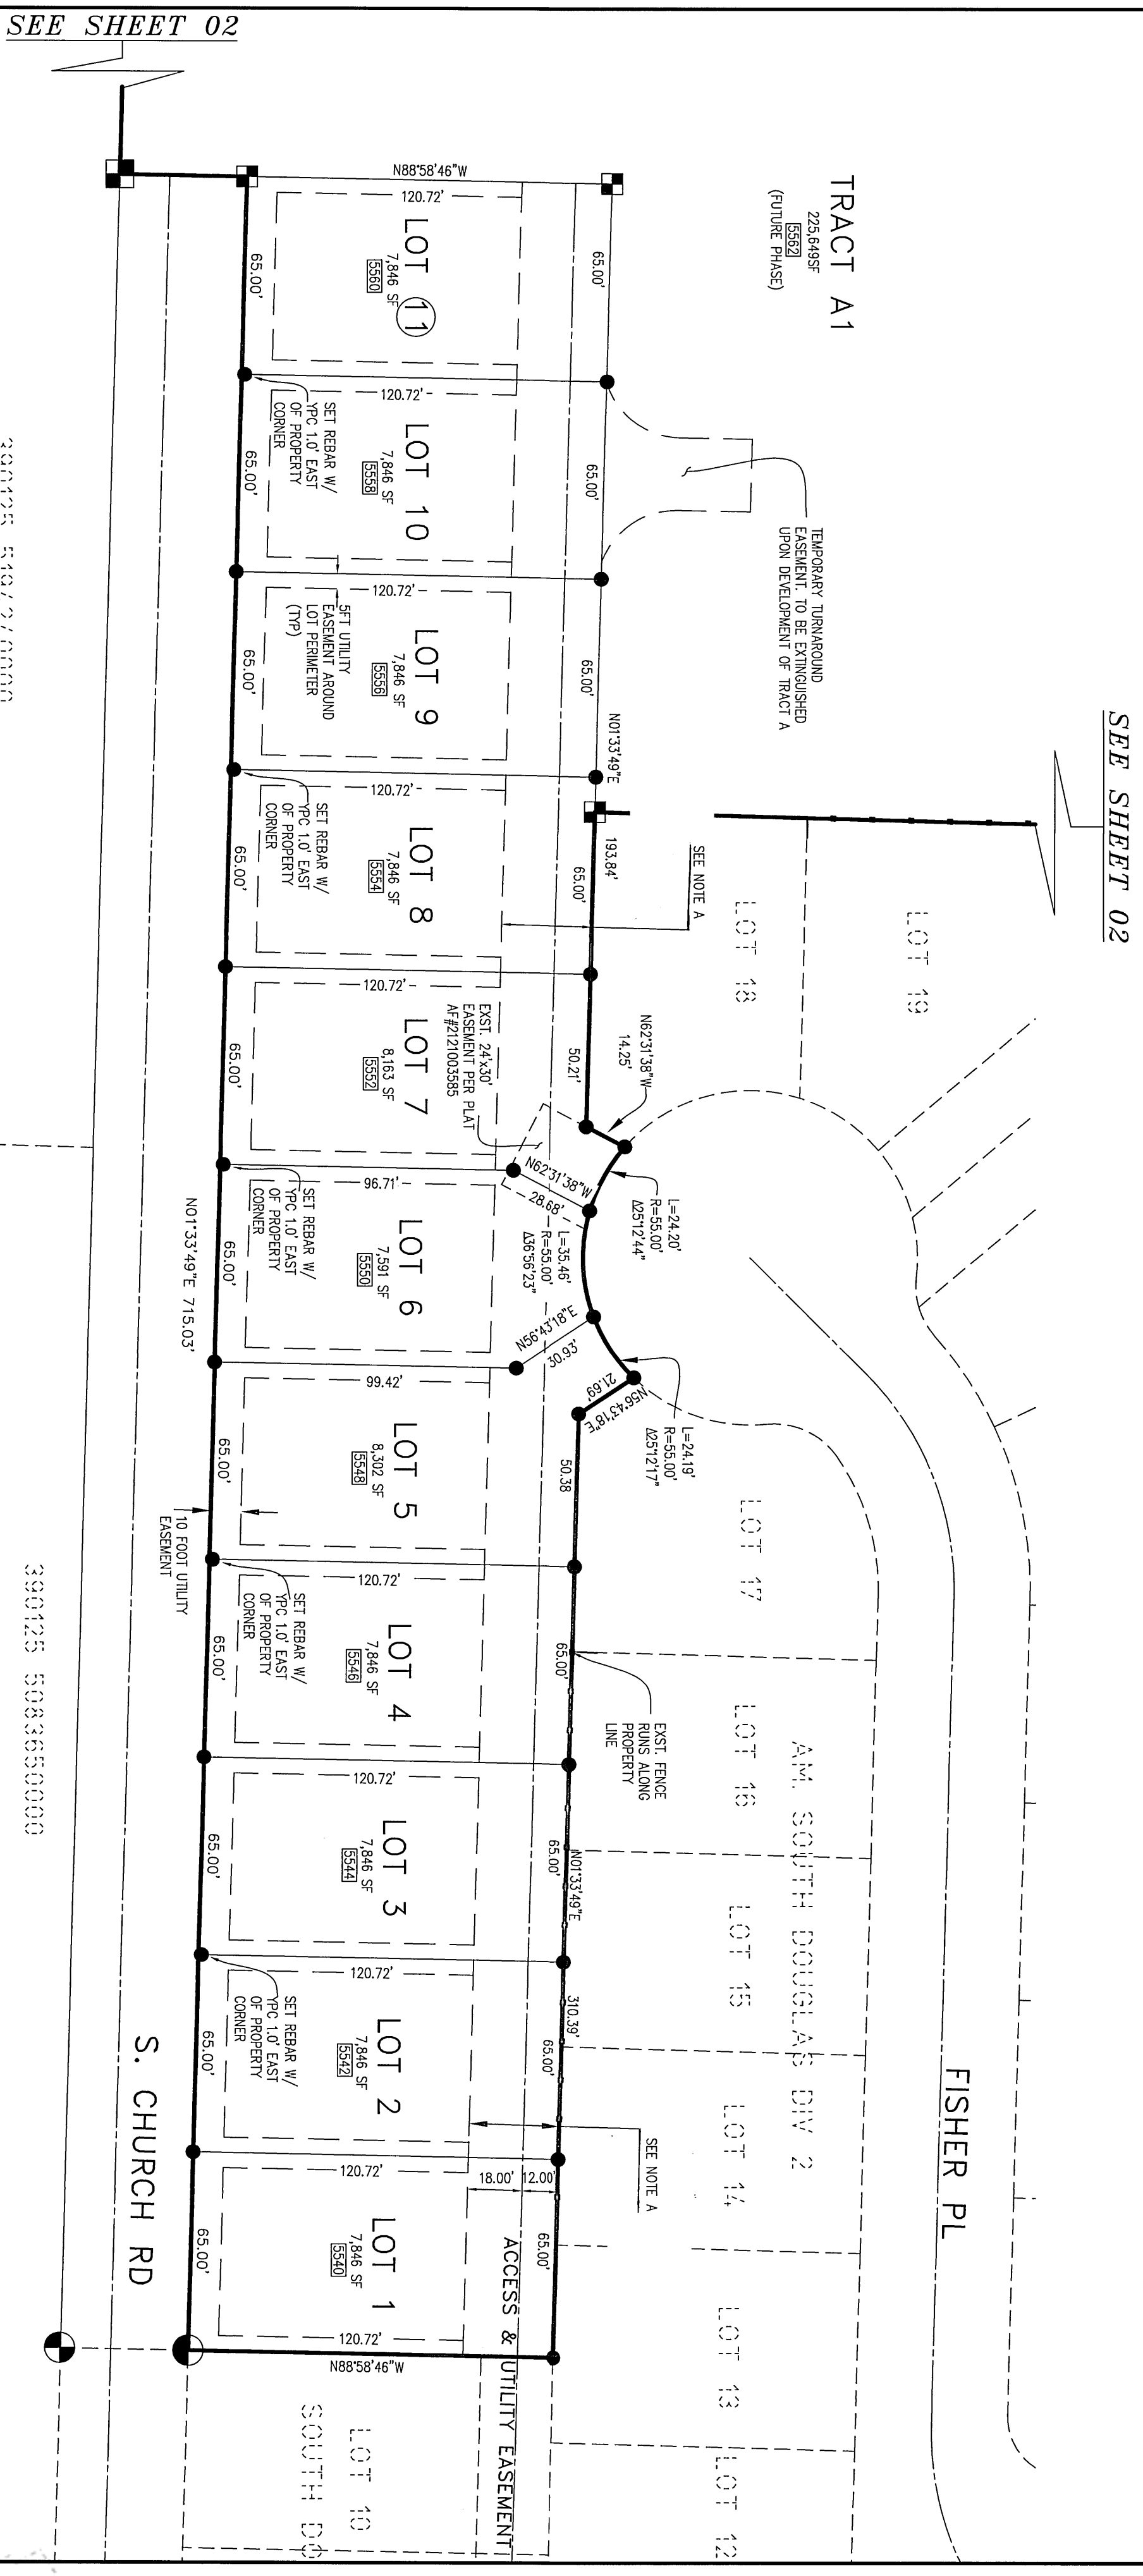


NOTE A
30-FOOT ACCESS AND UTILITY EASEMENT IN
FAVOR OF HOMEOWNERS ASSOCIATION AND SOUTH
CHURCH ROAD LOTS (AS DEFINED IN THE
DECLARATION OF COVENANTS, CONDITIONS,
RESERVATIONS AND RESTRICTIONS OF THE SOUTH
DOUGLAS LONG PLAT, DIV. 1)

LEGEND:

👤	= END BRASS MON (APRIL 2013)
👤	= END ALUMINUM CAP MON (APRIL 2013)
👤	= SETS 18" BRASS MON (APRIL 2013)
👤	= TIDES 18" YELLOW PLASTIC CAP MON (APRIL 2013)
👤	= FOUND BRASS W/YELLOW PLASTIC CAP MON (APRIL 2013)
👤	= MARKED "JEPSON 9351" MON. 2014
👤	= SET REBAR W/YELLOW PLASTIC CAP MON (APRIL 2013)
👤	= MARKED "TIDES IN 24218" MON. 2014
👤	= LOT ADDRESS

RG = RAIN GARDEN LOCATION

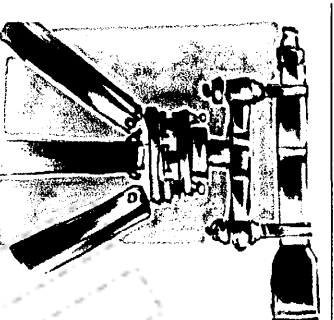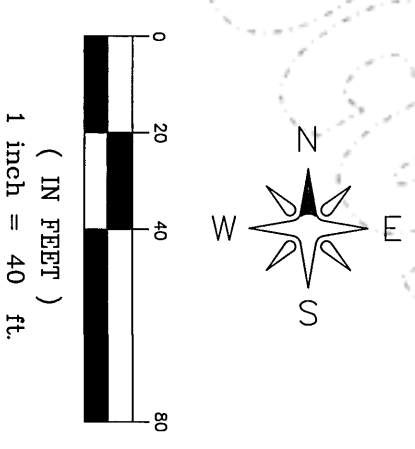

*LAND DEVELOPMENT
ENGINEERING & SURVEYING INC.*
5160 INDUSTRIAL PL. #108
FERNDALE, WA 98248
Ph (360), 383-0620

*LONG PLAT FOR:
SOUTH DOUGLAS, LLC*

JOB No. 13011	DWG No. 13011-PLAT.dwg	DATE: 02/04/15
DRN BY: SR	CHK BY: K.T.H.	SHEET 3 of 3