



00135699201808002760020025

PLAT:

South Douglas Division 4

Number of Pages: 2

Grantor (Declarants):

Kramer Construction Inc

Grantee: Public

Quarter: NW

Quarter: NW

Gov't Lot:

Section: 30

Township: 39N

Range: 02E

SOUTH DOUGLAS LONG PLAT DIVISION 4

BEING A PORTION OF THE NW 1/4 OF THE NW 1/4 OF SECTION 30, TOWNSHIP 39 NORTH, RANGE 2 EAST OF W.M.
CITY OF FERNDAL, WHATCOM COUNTY, WASHINGTON

PLAT NO. _____

LEGAL DESCRIPTION

(PER CHICAGO TITLE INSURANCE COMPANY GUARANTEE/CERTIFICATE NO. 245399671, DATED JANUARY 23, 2018)

TRACT A1, AS DELINEATED ON SOUTH DOUGLAS LONG PLAT, DIVISION 3, ACCORDING TO THE PLAT THEREOF, RECORDED FEBRUARY 12, 2015, UNDER AUDITOR'S FILE NO. 2150201460, RECORDS OF WHATCOM COUNTY, WASHINGTON.

SITUATE IN WHATCOM COUNTY, WASHINGTON.

DECLARATION AND DEDICATION

KNOWN TO ALL PERSONS BY THESE PRESENTS THAT WE THE UNDERSIGNED, BEING OWNERS IN FEE SIMPLE OF THE LAND HEREIN PLATTED, ARE PERSONS AUTHORIZED BY ALL PARTIES HAVING ANY INTEREST IN THE LAND HEREON DESCRIBED TO OBTAIN THIS PLAT, HEREBY DECLARE AND ACKNOWLEDGE THIS "SOUTH DOUGLAS LONG PLAT, DIVISION 4" AND DEDICATE TO THE USE OF THE PUBLIC FOREVER ALL ROADS AND/OR RIGHTS-OF-WAY OR OTHER AREAS AND OTHER WAYS; DO HEREBY WAIVE ON BEHALF OF THEMSELVES AND THEIR SUCCESSORS IN INTEREST ALL CLAIMS FOR DAMAGES AGAINST THE CITY OF FERNDAL AND ANY OTHER GOVERNMENTAL AUTHORITY WHICH MAY BE OCCASIONED TO THE ADJACENT LAND BY THE ESTABLISHED CONSTRUCTION, DRAINAGE AND MAINTENANCE OF SAID DEDICATED ROADS AND/OR RIGHTS-OF-WAY OR OTHER AREAS AND OTHER WAYS, AND DO HEREBY GRANT AND RESERVE ANY EASEMENTS SHOWN HEREON FOR THE USES INDICATED.

X William Kramer
KRAMER CONSTRUCTION, INC., WASHINGTON CORPORATION
WILLIAM KRAMER, PRESIDENT

Janice Kramer
KRAMER CONSTRUCTION, INC., WASHINGTON CORPORATION
JANICE KRAMER, VICE PRESIDENT

Grant Hauber Vice President OF PEOPLES BANK

ACKNOWLEDGEMENT

STATE OF WASHINGTON } SS
COUNTY OF WHATCOM }

I HEREBY CERTIFY THAT I KNOW OR HAVE SATISFACTORY EVIDENCE THAT WILLIAM KRAMER IS THE PERSON WHO APPEARED BEFORE ME, AND SAID PERSON ACKNOWLEDGED THAT HE SIGNED THIS INSTRUMENT, ON OATH STATED THAT HE WAS AUTHORIZED TO EXECUTE THE INSTRUMENT AND ACKNOWLEDGED IT AS THE PRESIDENT OF KRAMER CONSTRUCTION, INC., A WASHINGTON CORPORATION TO BE THE FREE AND VOLUNTARY ACT OF SUCH PARTY FOR THE USES AND PURPOSES MENTIONED IN THE INSTRUMENT.

GIVEN UNDER MY HAND AND OFFICIAL SEAL THIS 30 DAY OF July, 2018.

Chelsea J. Jenson
NOTARY PUBLIC IN AND FOR THE STATE OF WASHINGTON

RESIDING AT Bellingham, WA

ACKNOWLEDGEMENT

STATE OF WASHINGTON } SS
COUNTY OF WHATCOM }

I HEREBY CERTIFY THAT I KNOW OR HAVE SATISFACTORY EVIDENCE THAT JANICE KRAMER IS THE PERSON WHO APPEARED BEFORE ME, AND SAID PERSON ACKNOWLEDGED THAT SHE SIGNED THIS INSTRUMENT, ON OATH STATED THAT SHE WAS AUTHORIZED TO EXECUTE THE INSTRUMENT AND ACKNOWLEDGED IT AS THE VICE PRESIDENT OF SOUTH DOUGLAS DIVISION 4, A WASHINGTON LIMITED LIABILITY COMPANY, TO BE THE FREE AND VOLUNTARY ACT OF SUCH PARTY FOR THE USES AND PURPOSES MENTIONED IN THE INSTRUMENT.

GIVEN UNDER MY HAND AND OFFICIAL SEAL THIS 30 DAY OF July, 2018.

Chelsea J. Jenson
NOTARY PUBLIC IN AND FOR THE STATE OF WASHINGTON

RESIDING AT Bellingham, WA

ACKNOWLEDGEMENT

STATE OF WASHINGTON } SS
COUNTY OF WHATCOM }

I HEREBY CERTIFY THAT I KNOW OR HAVE SATISFACTORY EVIDENCE THAT Grant Hauber IS THE PERSON WHO APPEARED BEFORE ME, AND SAID PERSON ACKNOWLEDGED THAT (HE/SHE) SIGNED THIS INSTRUMENT, ON OATH STATED THAT (HE/SHE) WAS AUTHORIZED TO EXECUTE THE INSTRUMENT AND ACKNOWLEDGED IT AS THE Vice President OF PEOPLES BANK, TO BE THE FREE AND VOLUNTARY ACT OF SUCH PARTY FOR THE USES AND PURPOSES MENTIONED IN THE INSTRUMENT.

GIVEN UNDER MY HAND AND OFFICIAL SEAL THIS 1 DAY OF August, 2018.

Terry A. Unger
NOTARY PUBLIC IN AND FOR THE STATE OF WASHINGTON


RESIDING AT Bellingham

COVENANTS, CONDITIONS AND RESTRICTIONS

THE DECLARATION OF COVENANTS, CONDITIONS, RESTRICTIONS AND RESERVATIONS FOR "SOUTH DOUGLAS DIVISION 4 LONG PLAT" ARE RECORDED UNDER AUDITOR'S FILE NO. 2018-0800277


STORMWATER NOTES:

- ALL LOTS IN THIS LONG PLAT ARE EACH ALLOWED A TOTAL OF 2500 SQ. FT. OF IMPERVIOUS SURFACE WHICH INCLUDES ROOF AREA AND DRIVEWAYS.
- STORMWATER MANAGEMENT AND SITE DESIGN MUST BE DONE IN ACCORDANCE WITH THE STORMWATER SITE PLAN FOR DOUGLAS PLACE LONG PLAT AND SOUTH DOUGLAS LONG PLAT PREPARED BY RONALD T. JEPSON AND ASSOCIATES DATED MAY 2017.
- ALL DISRUPTED SOILS WITHIN THIS LONG PLAT SHALL BE AMENDED PER BMP T5.13 - POST CONSTRUCTION SOIL QUALITY AND DEPTH, PER THE AFOREMENTIONED STORMWATER SITE PLAN FOR DOUGLAS PLACE LONG PLAT AND SOUTH DOUGLAS LONG PLAT.
- BUILDING APPLICATIONS MUST INCLUDE DETAIL FOR BMP T5.13 POST CONSTRUCTION SOIL QUALITY AND DEPTH BEFORE SUBMITTAL. THE ENGINEER OF RECORD WILL CERTIFY INSTALLATION, INCLUDING SOILS ANALYSIS AND CERTIFICATION OF COMPOST AMENDMENT, PRIOR TO FINAL OCCUPANCY.
- INDIVIDUAL STORM SERVICE STUBS PROVIDED FOR THE DEVELOPED LOTS ARE FOR CRAWL SPACE POSITIVE AND PERIMETER DRAIN CONNECTION ONLY. ALL ROOF DRAINS AND DOWNSPOUTS WILL REQUIRE DOWNSPOUT SPLASH-BLOCK DISPERSION PER DETAIL 2-C45 ON THE APPROVED SOUTH DOUGLAS, DIVISION 4 AS-BUILTS. ROOF DRAINS MAY NOT CONNECT TO THE ONSITE STORM SYSTEM INDICATED IN THE APPROVED STORMWATER REPORT FOR SOUTH DOUGLAS, DIVISION 4.
- DRIVEWAYS SHALL BE POSITIVELY GRADED TO SHEET FLOW STORMWATER RUNOFF ACROSS LAWNS BEFORE ENTERING THE STORM DRAIN SYSTEM.

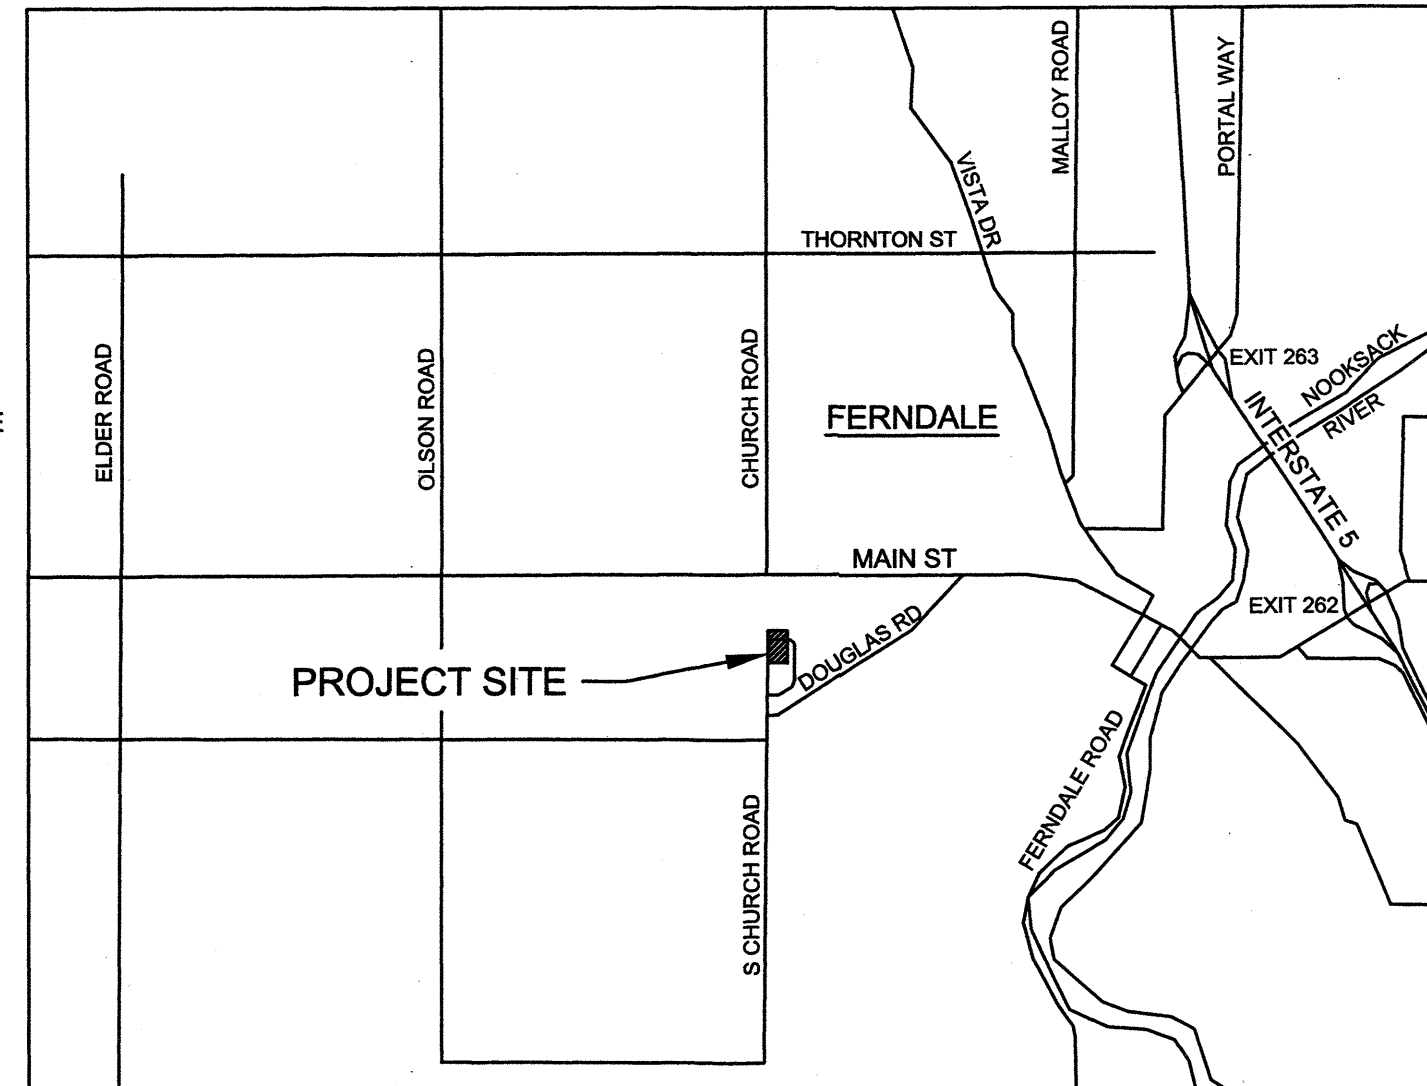

VICINITY MAP - FERNDAL

NTS

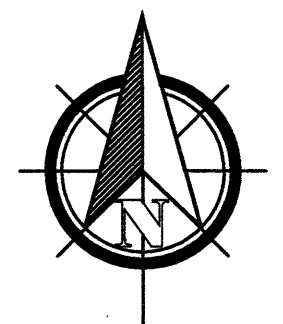

NOT TO SCALE

REFERENCE SURVEYS:

NAME	AF NO.
RECORD OF SURVEY DOUGLAS ROAD LLA	931119056 2070801956
SOUTH DOUGLAS LONG PLAT, DIV 1	2090102033
SOUTH DOUGLAS LONG PLAT, DIV 2	2120200446
AMD. SOUTH DOUGLAS LONG PLAT, DIV 2	2121003585
SOUTH DOUGLAS LONG PLAT, DIV 3	2150201460

MAINTENANCE AGREEMENT

ALL COSTS TO MAINTAIN, REPAIR, IMPROVE ANY STORMWATER FACILITY, DESIGNATED WETLAND, OPEN SPACE TRACT, OR OTHER COMMON FACILITIES OR OPEN SPACE ELEMENTS LOCATED OUTSIDE PUBLIC RIGHT-OF-WAY SHALL BE BORNE BY THE HOMEOWNERS' ASSOCIATION ACCORDING TO THE COVENANTS, CONDITIONS, RESERVATIONS, AND RESTRICTIONS (CC&R'S) OF SOUTH DOUGLAS LONG PLAT DIVISION 4, AS RECORDED UNDER AUDITOR'S FILE NO. 2018-0800277, RECORDS OF WHATCOM COUNTY, WASHINGTON.

NOTES:

- ALL OR ANY LOTS REQUIRING MORE THAN THE 1-FOOT MINIMUM FILL AMOUNT WILL REQUIRE STRUCTURAL FILL DOCUMENTATION BY A LICENSED GEOTECHNICAL ENGINEER.
- ALL LOTS HAVE A 10' UTILITY EASEMENT ADJACENT TO PUBLIC RIGHT-OF-WAYS AND A 5' UTILITY EASEMENT ALONG ALL OTHER SIDES UNLESS A WIDER EASEMENT IS SHOWN ON THE PLAN.
- FUTURE LOT OWNERS SHALL COMPLY WITH APPENDIX "J" INTERNATIONAL BUILDING CODE REQUIREMENTS.
- HALF OF THE TRAFFIC, PARK AND SCHOOL IMPACT FEES HAVE BEEN PAID, THE REMAINING HALF SHALL BE PAID PURSUANT TO BUILDING PERMIT CONDITIONS OF APPROVAL. SCHOOL IMPACT FEES SHALL BE PAID IN ACCORDANCE WITH THE REQUIREMENTS OF THE FERNDAL SCHOOL DISTRICT. STORM SEWER MITIGATION FEES PER SQUARE FOOT OF GROSS PROPERTY AREA HAVE BEEN PAID. WATER AND SEWER CONNECTION FEES SHALL BE PAID PURSUANT TO BUILDING PERMIT CONDITIONS OF APPROVAL.
- SUBJECT TO RECIPROCAL STORMWATER FACILITIES EASEMENT FILED UNDER AUDITOR'S FILE NO. 2090102035.
- SUBJECT TO PUGET SOUND ENERGY EASEMENT FILED UNDER AUDITOR'S FILE NO. 2071002258.
- SUBJECT TO MAINTENANCE COVENANT AND ACCESS EASEMENT FILED UNDER AUDITOR'S FILE NO. 2111200745.
- ALL STRUCTURES INCLUDING BUILDING FOUNDATIONS ON LOTS 18 AND 19 MUST BE SET BACK A MINIMUM OF 15' FROM WATER AND SEWER MAINS. NO PERMANENT OR TEMPORARY STRUCTURES WILL BE CONSTRUCTED WITHIN THE 30-FOOT UTILITY EASEMENT.

PUBLIC WORKS DIRECTOR'S APPROVAL

EXAMINED AND APPROVED BY THE CITY OF FERNDAL DEPARTMENT OF PUBLIC WORKS AS TO THE SURVEY DATA, LAYOUT OF ROADS AND OTHER RIGHT-OF-WAYS THIS 2nd DAY OF August, 2018.

[Signature]
PUBLIC WORKS DIRECTOR, CITY OF FERNDAL, WASHINGTON

PLAT ADMINISTRATOR'S APPROVAL

EXAMINED AND APPROVED BY THE CITY OF FERNDAL PLAT ADMINISTRATOR THIS 2nd DAY OF August, 2018.

[Signature]
PLAT ADMINISTRATOR, CITY OF FERNDAL, WASHINGTON

CITY CLERK'S APPROVAL

THIS PLAT APPROVED AND ROADS ACCEPTED BY ORDER OF THE CITY CLERK OF FERNDAL, WASHINGTON THIS 2nd DAY OF August, 2018.

[Signature]
CITY CLERK, CITY OF FERNDAL, WASHINGTON

WHATCOM COUNTY TREASURER'S CERTIFICATE

I, STEVE OLIVER, TREASURER OF WHATCOM COUNTY, WASHINGTON, DO HEREBY CERTIFY THAT ALL TAXES REQUIRED BY LAW TO BE PAID UPON THE REAL ESTATE EMBRACED WITHIN THIS PLAT OF "SOUTH DOUGLAS LONG PLAT DIVISION 4" AND ALL DELINQUENT ASSESSMENTS HAVE BEEN FULLY PAID. AS SHOWN IN THE RECORDS OF MY OFFICE, THIS 2nd DAY OF August, 2018.

[Signature]
TREASURER
WHATCOM COUNTY WASHINGTON



AUDITOR'S CERTIFICATE

FILED FOR RECORD THIS 2nd DAY OF August, 2018

AT 3:56 P.M. IN BOOK _____ OF SURVEYS ON PAGE _____

AT THE REQUEST OF _____ JEPSON & ASSOCIATES


Debbie Adelman by Kynal
COUNTY AUDITOR

AUDITOR'S FILE NO. 2018-0800276


LAND SURVEYOR CERTIFICATION

THIS MAP CORRECTLY REPRESENTS A SURVEY MADE BY ME OR UNDER MY DIRECTION IN CONFORMANCE WITH THE REQUIREMENTS OF THE SURVEY RECORDING ACT AT THE REQUEST OF WILLIAM KRAMER IN JUNE, 2017.

[Signature]
RONALD T. JEPSON L.S. NO. 9361 8/1/18

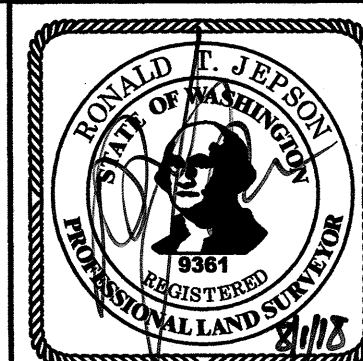

PREPARED FOR:
SOUTH DOUGLAS, LLC

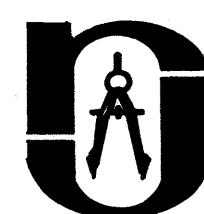

RONALD T. JEPSON & ASSOC.
REGISTERED PROFESSIONAL ENGINEERS AND LAND SURVEYORS
222 GRAND AVE., SUITE C, BELLINGHAM, WA 98225
PHONE: (360) 733-5760
FAX: (360) 647-8939
EMAIL: RJEPSON@JEPSONENGINEERING.COM

SOUTH DOUGLAS LONG PLAT DIVISION 4



PTN. NW 1/4 NW 1/4, SEC. 30, TWP. 39 N., RGE. 2 E. W.M.
CITY OF FERNDAL, WHATCOM COUNTY, WA.

JOB NO: 15043.01	ISSUE DATE: 07/27/2018	SHEET NO.: 1 of 2
DRAWN BY: MGS	CHECKED BY: RTJ	

SOUTH DOUGLAS LONG PLAT DIVISION 4

PLAT NO. _____


BEING A PORTION OF THE NW 1/4 OF THE NW 1/4 OF SECTION 30, TOWNSHIP 39 NORTH, RANGE 2 EAST OF W.M.
CITY OF FORDABLE, WHATCOM COUNTY, WASHINGTON

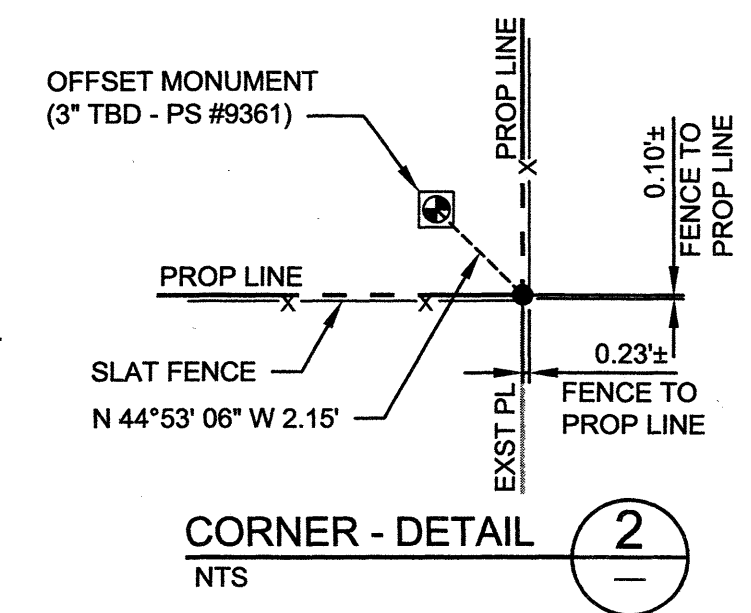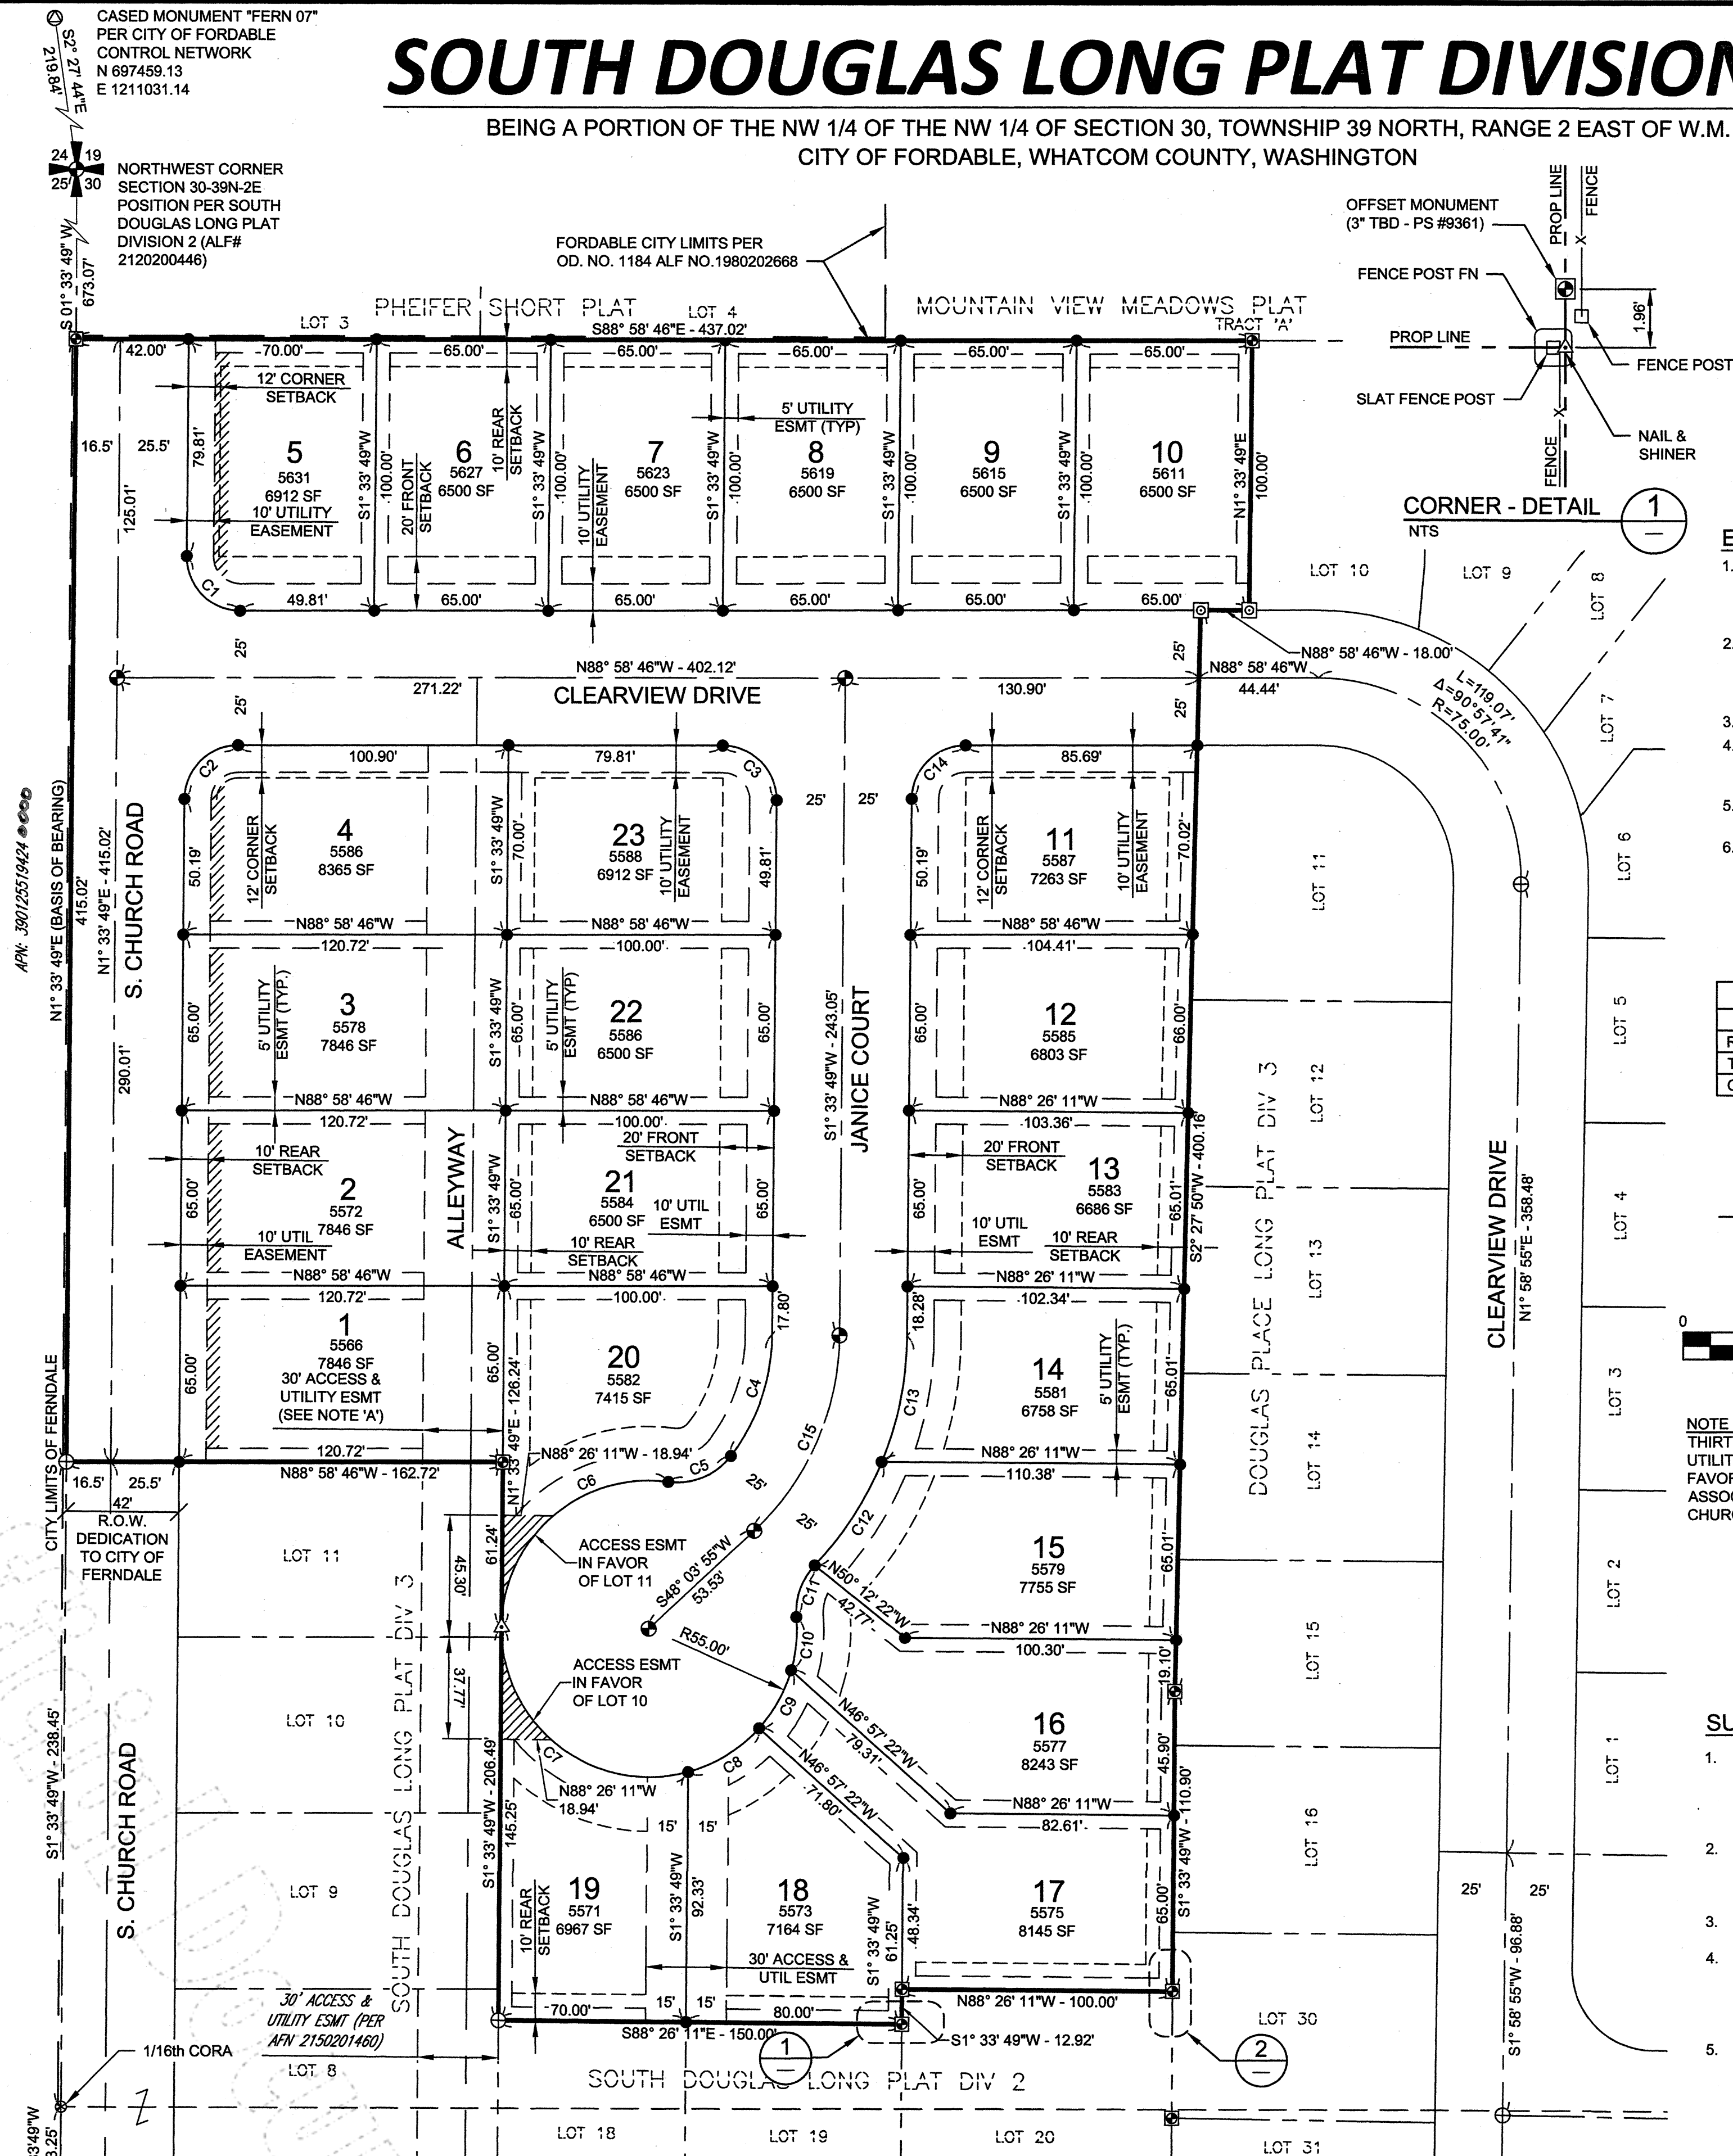

EASEMENT & SETBACK NOTES:

1. ALL LOTS HAVE A 10' UTILITY EASEMENT ADJACENT TO PUBLIC RIGHT-OF-WAYS AND A 5' UTILITY EASEMENT ALONG ALL OTHER SIDES UNLESS A WIDER EASEMENT IS SHOWN ON THE PLAN.
2. THERE IS A 20' (TYPICAL) SET BACK FOR ALL PROPERTIES ADJACENT TO PUBLIC RIGHT-OF-WAYS WITH THE EXCEPTION OF THE NORTH SIDE OF LOTS 4, 11 & 23 WHICH HAVE A 12' CORNER SETBACK.
3. ALL OTHER SETBACKS ARE TYPICALLY 10'.
4. THE ALLEYWAY BETWEEN JANICE COURT AND CHURCH ROAD LIES WITHIN A 30' ACCESS AND UTILITY EASEMENT ON THE EAST SIDE OF LOTS 1 THROUGH 4.
5. THERE IS A 30' ACCESS AND UTILITY EASEMENT OVER LOTS 18 AND 19 (PRIMARILY FOR UTILITIES ACCESS).
6. THERE ARE TWO TRIANGULAR ACCESS EASEMENTS ON THE WEST SIDE OF THE CUL-DE-SAC. THE NORTH EASEMENT IS OVER LOT 20 AND IN FAVOR OF LOT 11. THE SOUTH EASEMENT IS OVER LOT 19 AND IN FAVOR OF LOT 10. BOTH LOT 10 & LOT 11 ARE A PART OF AND RESIDE WITHIN THE SOUTH DOUGLAS HORN PLAT, DIVISION 3.

DENSITY TABLE		
	ACRES & SQUARE FOOTAGE	PERCENT
R.O.W. DEDICATION	1.40 ACRES (61,125 SQ. FT.)	27.06%
TOTAL LOT AREA	3.78 ACRES (164,767 SQ. FT.)	72.94%
OVERALL PARCEL AREA	5.18 ACRES (225,884 SQ. FT.)	100%

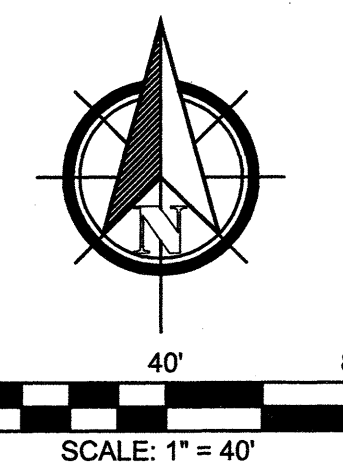

NOTE 'A':
THIRTY FOOT ACCESS AND
UTILITY EASEMENT IN
FAVOR HOMEOWNER'S
ASSOCIATION AND SOUTH
CHURCH ROAD LOTS.


CURVE TABLE			
CURVE	LENGTH	RADIUS	DELTA
C1	31.61'	20.00'	90°32'35"
C2	31.23'	20.00'	89°27'25"
C3	31.60'	20.00'	90°32'11"
C4	48.29'	75.00'	36°53'21"
C5	26.30'	25.00'	60°17'03"
C6	93.28'	55.00'	97°10'31"
C7	101.59'	55.00'	105°49'37"
C8	31.38'	55.00'	32°41'35"
C9	24.84'	55.00'	25°52'20"
C10	19.85'	55.00'	20°40'43"
C11	20.98'	25.00'	48°04'46"
C12	45.95'	125.00'	21°03'46"
C13	47.88'	125.00'	21°56'47"
C14	31.23'	20.00'	89°27'25"
C15	81.16'	100.00'	46°30'10"

SURVEY NOTES:


1. STANDARD FIELD TRAVERSE PROCEDURES WERE PERFORMED WITH A LEXICAL 1203 ROBOTIC TOTAL STATION FOR THIS SURVEY. THE ACCURACY OF SAID INSTRUMENT MEETS OR EXCEEDS THOSE PRECISION STANDARDS STATED IN WAC 332-130-090.
2. THE FIELD WORK PERFORMED FOR THIS SURVEY WAS COMPLETED OCTOBER 18, 2017. ALL MONUMENTS SHOWN HEREON WERE VISITED DURING THE COURSE OF THIS SURVEY UNLESS OTHERWISE NOTED.
3. HORIZONTAL DATUM: CITY OF FORDABLE SURVEY CONTROL NETWORK (NAD 83/91).
4. BASIS OF BEARINGS: DOUGLAS PLACE LONG PLAT DIVISION NO. 22, ACCORDING TO THE PLAT THEREOF, RECORDED OCTOBER 22, 2013, UNDER AUDITOR'S FILE NO. 2131002302, RECORDS OF WHATCOM COUNTY, WASHINGTON.
LINE HELD: N 01° 33' 49" E - 2,653.07' (WEST LINE OF SECTION 30)
5. THIS SURVEY DEPICTS OCCUPATIONAL INDICATORS IN ACCORDANCE WITH WAC 332.130. THESE OCCUPATIONAL INDICATORS MAY INDICATE A POTENTIAL CLAIM OF UNWRITTEN OWNERSHIP. THE LEGAL RESOLUTION OF SUCH CLAIMS HAS NOT BEEN RESOLVED BY THIS SURVEY.

LEGEND

- | | | | |
|---|---|---|---|
|  | FOUND PLAT BOUNDARY MONUMENT
[CAPPED REBAR IN CONCRETE] (PS NO.
18927), AUGUST 2017 |  | SET 2" BRASS DISK (CENTERLINE
RIGHT-OF-WAY MONUMENT) PS NO. 9361 |
|  | SET PLAT BOUNDARY MONUMENT [3"
BRASS DISK IN CONCRETE] (PS NO. 9361) |  | SET CAPPED REBAR (PS NO. 9361) ON
JAN 2 THRU FEB 19, 2018. |
|  | FOUND 2" BRASS DISK (CENTERLINE
RIGHT-OF-WAY MONUMENT) PS NO. 9361 |  | SET NAIL & SHINER (PS NO. 9361) |
| | |  | CALCULATED 1/16th CORNER LOCATION |

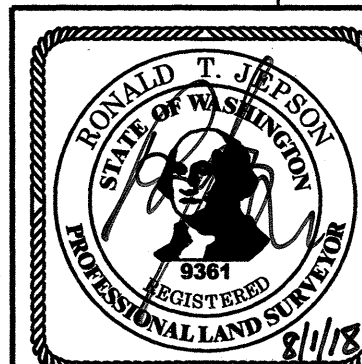

PREPARED FOR:
SOUTH DOUGLAS, LLC

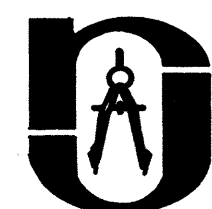

RONALD T. JEPSON & ASSOC.
REGISTERED PROFESSIONAL ENGINEERS AND LAND SURVEYORS
222 GRAND AVE., SUITE C, BELLINGHAM, WA 98225
PHONE: (360) 733-5760
FAX: (360) 647-8939
EMAIL: RJEPSON@JEPSONENGINEERING.COM

**SOUTH DOUGLAS
LONG PLAT DIVISION 4**

PTN. NW 1/4 NW 1/4, SEC. 30, TWP. 39 N., RGE. 2 E. W.M.
CITY OF FORDABLE. WHATCOM COUNTY. WA.

JOB NO: 15043.01	ISSUE DATE: 07/27/2018	SHEET NO.:
---------------------	---------------------------	------------

DRAWN BY: MCS	CHECKED BY: PTJ	2 of 2
------------------	--------------------	--------

2 of 2